bolig og planstyrelsen

Version 1.~~1~~2 med ændringsmarkeringer i forhold til version 1.1

08-02-2023

Bygningsreglementets vejledning til kapitel 5 - Brand

Bilag 11 - Præ-accepterede løsninger for ~~midlertidige transportable~~ forsamlingstelte, midlertidige camping-områder og midlertidige udendørs salgsområder

Indholdsfortegnelse

1 Indledning ... 3
2 Forsamlingstelte ... 6
2.1 Myndighedsbehandling ... 6
2.1.1 Meddelelse til kommunalbestyrelsen ... 7
2.1.2 Midlertidig overnatning i forsamlingstelte ... 7
2.2 Indplacering i anvendelseskategorier, risikoklasser og brandklasser ... 7
2.3 Certificeret brandrådgiver og statiker ... 8
2.4 Teknisk sagsbehandling ... 9
2.5 Evakuering og redning af personer ... 9
2.5.1 Generelt ... 9
2.5.2 Evakuering ... 9
2.5.3 Flugtveje herunder antal, udformning, sikring og sikring af brug ... 9
2.5.4 Udgange ... 10
2.5.5 Udformning af udgange ... 10
2.5.6 Pladsfordelingsplaner ... 12
2.6 Antændelse, brand og røgspredning ... 13
2.6.1 Generelt ... 13
2.6.2 Placering af forsamlingstelte ... 13
2.6.3 Indvendige og udvendige overflader ... 14
2.6.4 Risiko for antændelse ... 14
2.7 Brandtekniske installationer i forsamlingstelte ... 15
2.7.1 Varsling ... 16
2.7.2 Flugtvejs- og panikbelysning ... 16
2.7.3 Brandslukningsudstyr ... 16
2.7.4 Automatisk sprinkleranlæg ... 17
2.8 Brandmodstandsevne for bærende konstruktioner ... 17
2.8.1 Brandmodstandsevne ... 17
2.9 Ordensregler for forsamlingstelte ... 17
3 Midlertidige campingområder ... 19
3.1 Myndighedsbehandling ... 19
3.1.1 Campingområder til højst 150 personer ... 19
3.1.2 Campingområder til flere end 150 personer ... 19
3.2 Indretning af campingområder ... 20
3.2.1 Teltområder ... 21
3.2.2 Caravanområder ... 21
3.2.3 Blandede områder ... 22
3.3 Udarbejdelse af planer for campingområder ... 22

Med ændringsmarkeringer i forhold til version 1.1

Version 1.~~1~~2 med ændringsmarkeringer i forhold til version 1.1

08-02-2023

3.4 Opvarmning 22
3.5 Anvendelse af kogeapparater 22
3.6 F-gas 23
3.7 Kulgrill, bål og brug af åben ild 23
3.8 Håndslukningsudstyr 23
3.9 Ordensregler for campingområder 23
4 Midlertidige udendørs salgsområder 25
4.1 Myndighedsbehandling 25
4.1.1 Udendørs salgsområder til højst 150 personer 25
4.1.2 Udendørs salgsområder til flere end 150 personer 25
4.2 Indretning af salgsområder 27
4.2.1 Opdeling af salgsområder 27
4.3 Udarbejdelse af planer for salgsområder 28
4.4 Udgange og flugtveje 29
4.4.1 Fra salgsboder 29
4.4.2 Fra salgsområder 29
4.4.3 Opvarmning 29
4.5 Anvendelse af kogeapparater 29
4.6 F-gas 29
4.7 Kulgrill, bål og brug af åben ild 30
4.8 Håndslukningsudstyr 30
4.8.1 Ordensregler for salgsområder 30
5 Drift, kontrol og vedligehold 32
5.1 Driftsjournal 32
5.2 Brand- og evakueringsinstruks 33
5.3 Ordensregler om forebyggelse af brand 33
6 Redningsberedskabets indsatsmuligheder 34
6.1 Midlertidige arrangementer 34
6.2 Øvrig bebyggelse 34
Anneks A Tabel til forsamlingstelte til private formål 36
Anneks B Tabel til forsamlingstelte til ikke private formål 37

Med ændringsmarkeringer i forhold til version 1.1

1 Indledning

Dette bilag til *BR18 - Bygningsreglementets vejledning til kapitel 5 – Brand* kan anvendes ved midlertidig opstilling af ~~transportable~~ forsamlingstelte og etablering af midlertidige udendørs campingområder~~ og~~samt midlertidige udendørs salgsområder. Ved midlertidighed i dette bilag forstås en varighed på højst 6 uger. Der vil dog i bilaget ikke altid blive nævnt "midlertidig", når der henvises til midlertidig opstilling af ~~transportable~~ forsamlingstelte~~,~~ samt midlertidige udendørs camping- og salgsområder.

Dette bilag har til formål at beskrive præ-accepterede løsninger for brandsikring af midlertidig opstilling af ~~transportable~~ forsamlingstelte, og etablering af midlertidige udendørs camping- og salgsområder. De p~~P~~ræ-accepterede løsninger~~, er løsninger der, når de anvendes i deres helhed,~~ sikrer, at Bygningsreglementets brandkrav overholdes, når løsningerne anvendes i deres helhed~~krav overholdes~~.

Eksisterende c~~C~~amping- og salgsområder, der tidligere har fået ~~en~~ tilladelse til at afholde et arrangement efter Bygningsreglementet *BR18* ~~eller~~, Beredskabsstyrelsens "*Tekniske forskrifter for forsamlingstelte, selskabshuse, salgsområder og campingområder, der ikke er omfattet af campingreglementet*" af 18. oktober 2005, eller *Bekendtgørelse nr. 1382 af 15. december 2014 om brandværnsforanstaltninger for forsamlingstelte, salgsområder og campingområder, der ikke er omfattet af campingreglementet* kan anvende forudsætningerne i ~~denne~~ tilladelsen på samme ~~vis~~ måde som de præ-accepterede løsninger i dette bilag. Det kræver dog, at forudsætningerne for tilladelsen samt eventuelle vilkår i tilladelsen følges i ~~sin~~ deres helhed, og at arrangementet afholdes på samme lokation som tilladelsen er givet til.

Billaget indeholder tillige gennerelle retningslinjer for opstilling af certificerede transportable konstruktioner der opsættes som forsamlingstelte eller i forbindelse med midlertidige campingområder og midlertidige udendørs salgsområder. En certificeret transportabel konstruktion er en konstruktion der er certificeret i henhold til Bekendtgørelse nr. 673 af 1. juli 2021, Bekendtgørelse om certificeringsordning for transportable konstruktioner.

Bilaget er opdelt i følgende seks afsnit~~:~~:

1. Indledning
2. ~~Transportable f~~Forsamlingstelte
3. Midlertidige ~~C~~campingområder
4. Midlertidige udendørs ~~S~~salgsområder
5. Drift, kontrol og vedligehold
6. Redningsberedskabets indsatsmuligheder

I afsnittene 2, 3 og 4 er der præ-accepterede løsninger, som beskriver hvordan de enkelte områder kan indrettes. De tre afsnit kan stå alene, dog i sammenhæng med afsnit 5 og 6, som skal følges for de tre afsnit.

Ved arrangementer, der omfatter forsamlingstelte, camping- og salgsområder~~,~~ og eventuelt andre områder, ~~der~~ som ikke er omfattet af dette bilag, ~~såsom~~ f.eks.~~x~~ koncertområder foran scener, forlystelser, parkeringsarealer ~~m.m.~~, skal der udarbejdes en arrangementsplan, der giver et samlet overblik over de enkelte områder~~,~~ og redningsberedskabets muligheder for at ~~kunne~~ komme frem på området.

Arrangementsplanen er en del af den dokumentation, der skal indsendes til kommunen mindst 4 uger før et forsamlingstelt eller~~,~~ et camping- eller ~~et~~ salgsområde til flere end 150 personer tages i brug, og skal angive placering, indretning og brug af de enkelte delområder. Arrangementsplanen bør udarbejdes i henhold til denne vejlednings *B~~b~~ilag 11a: Vejledning om arrangementsplaner for midlertidige udendørsarrangementer*.

Med ændringsmarkeringer fra høringsversion 1.1

Placering af gasflasker, der forsyner anlæg eller er reserveflasker hertil, skal opfylde reglerne i *Beredskabsstyrelsens Bekendtgørelse nr. 1444 af 15. december 2010 om tekniske forskrifter for gasser*, som ændret ved *Bekendtgørelse nr. 230 af 16. marts 2011, bekendtgørelse nr. 588 af 1. juni 2016, bekendtgørelse nr. 1421 af 4. december 2017* og *bekendtgørelse nr. 981 af 22. juni 2022.*

Hvis der skal søges byggetilladelse, skal det som udgangspunkt ske via den digitale løsning som kommunen anvender. Hvis kommunen finder, at der foreligger særlige forhold, der gør, at ansøgeren eller anmelderen ikke forventes at kunne anvende digital selvbetjening, skal kommunalbestyrelsen tilbyde, at ansøgningen eller anmeldelsen kan indgives på anden måde end digital selvbetjening. Kommunalbestyrelsen bestemmer, hvordan en ikke-digital ansøgning eller anmeldelse skal indgives.

1.1 Definition af telte

Definition af telte indeholdt i dette bilag:


- Forsamlingstelte er telte eller overdækninger med teltdug, indrettet som et samlet rum, der benyttes til dagopholdsfunktioner for flere end 50 personer og højst 1.000 personer og/eller er større end 50 m^2. Forsamlingstelte på højst 100 m^2 kan benyttes til midlertidig overnatning af højst 50 personer. Forsamlingstelte er omfattet af afsnit *2.*
- Campingtelte er telte eller overdækninger med teltdug, der benyttes til camping herunder overnatning for højst 50 personer og/eller højst er 50 m^2. Campingtelte er omfattet af afsnit *3.*
- Salgstelte er telte eller overdækninger med teltdug på højst 100 m^2, der anvendes som salgsbod eller lignende til højst 50 personer. Salgstelte er omfattet af afsnit *4.*

Opstilling af forsamlingstelte og overdækninger med teltdug i én etage på højst 50 m^2 og/eller beregnet til højst 50 personer er kun omfattet af de funktionsbaserede krav i BR18 § 82 uden præskriptive bestemmelser, og er dermed ikke omfattet af dette bilag.

På næste side er vist et flowdiagram, som angiver, hvilken dokumentationsform der er gældende for forsamlingstelte, salgstelte på udendørs midlertidige salgsområder og campingtelte på midlertidige campingområder afhængig af bl.a. teltets anvendelse og størrelse, om teltet er certificeret, antal personer i teltet, om det er et offentligt eller privat arrangement og om de præ-accepterede løsninger i dette bilag følges.

I *Anneks A* er angivet tabel med præ-accepterede løsninger for forsamlingstelte til private formål, og i *Anneks B* er angivet tabel med præ-accepterede løsninger for forsamlingstelte til ikke private formål.

Med ændringsforslag i høring 2. version 1.1

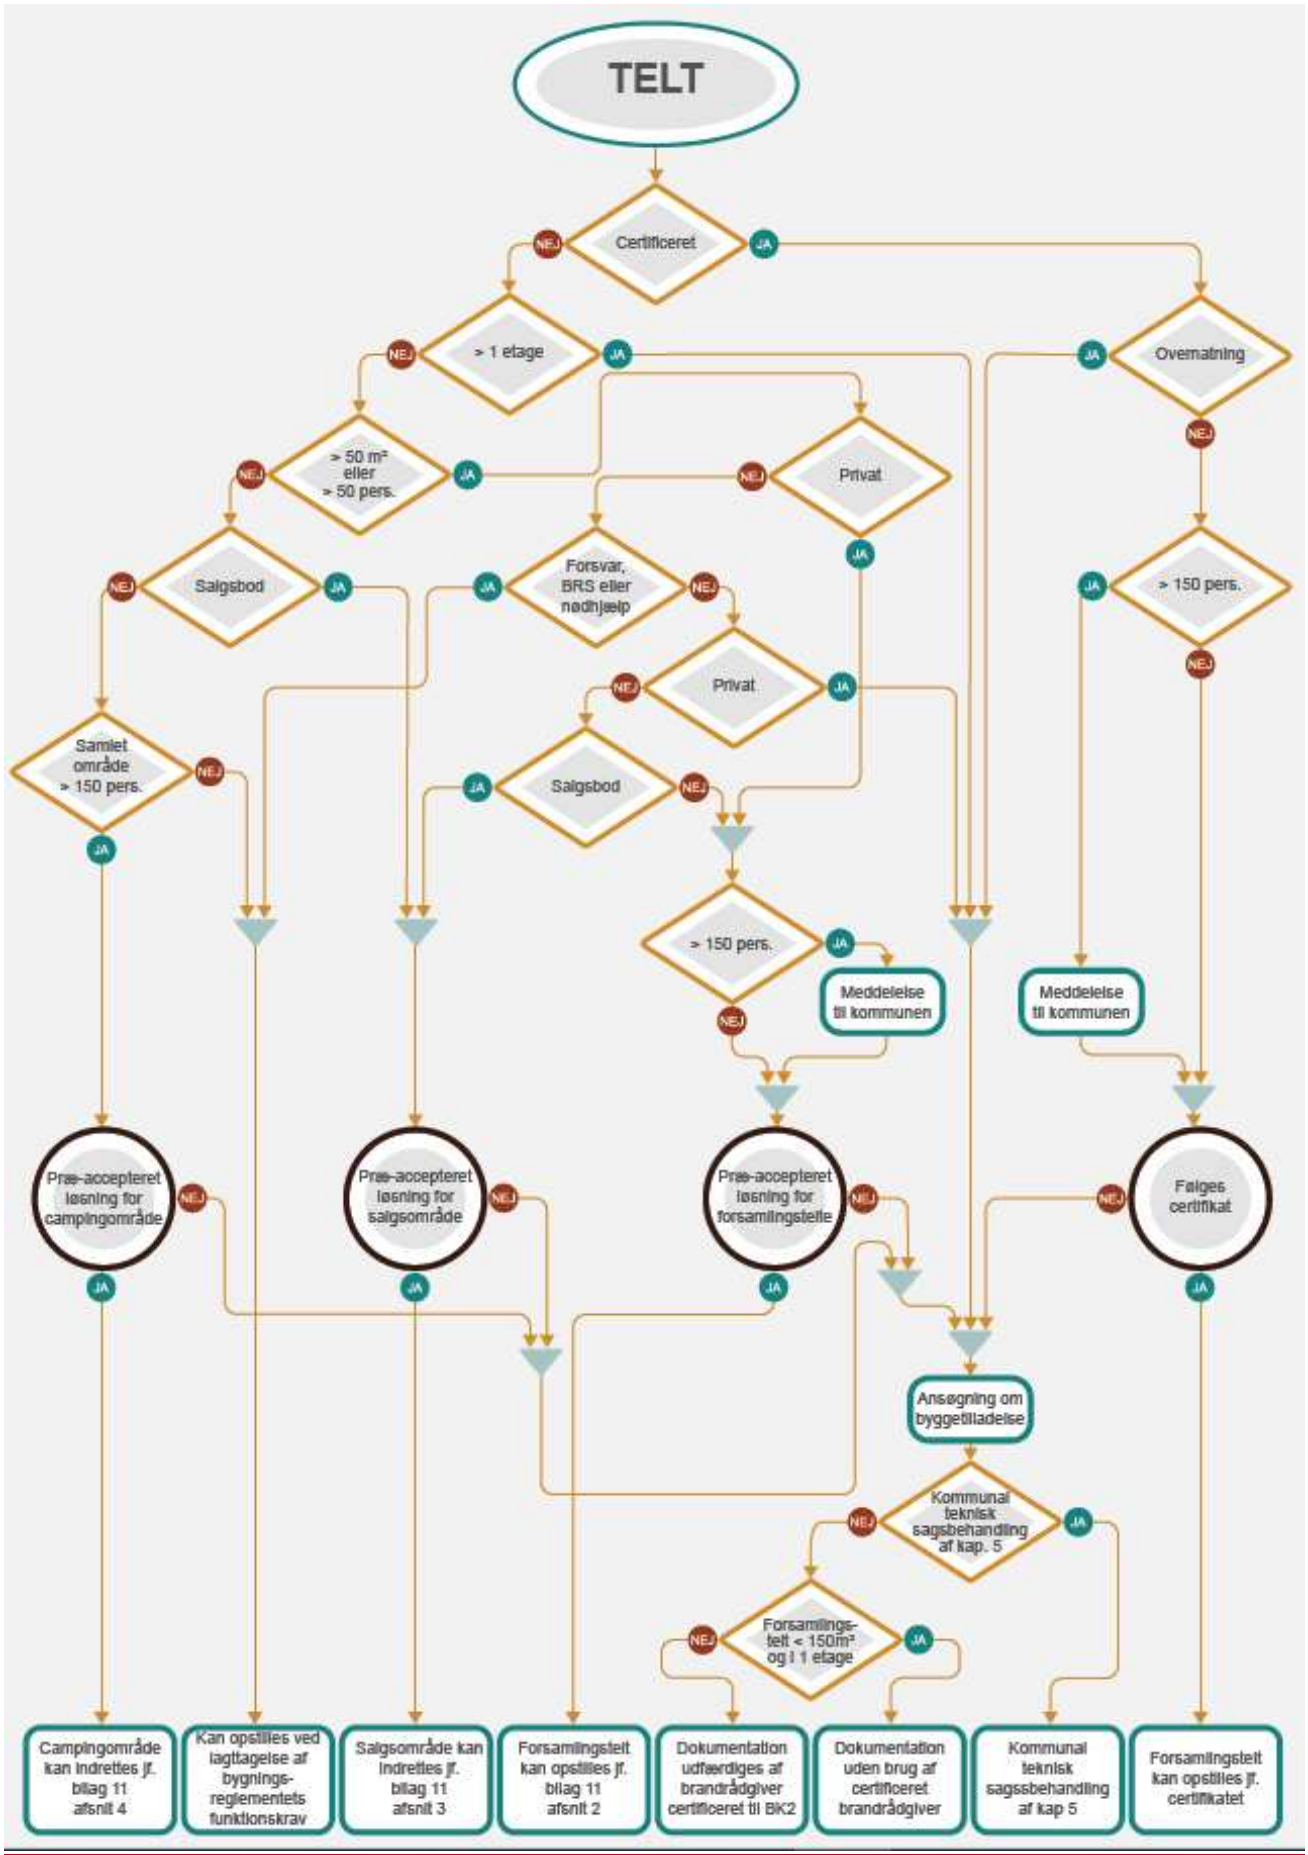
TELT
Certificeret
NEJ
JA
> 1 etage
Overnatning
> 50 m² eller > 50 pers.
Privat
Salgsbod
Forsvar, BRS eller nødhjælp
> 150 pers.
Samlet område > 150 pers.
Meddelelse til kommunen
Præ-accepteret løsning for campingområde
Præ-accepteret løsning for salgsområde
Præ-accepteret løsning for forsamlingstelte
Følges certifikat
Ansøgning om byggetilladelse
Kommunal teknisk sagsbehandling af kap. 5
Forsamlings-telt < 150m² og i 1 etage
Campingområde kan indrettes jf. bilag 11 afsnit 4
Kan opstilles ved iagttagelse af bygnings-reglementets funktionskrav
Salgsområde kan indrettes jf. bilag 11 afsnit 3
Forsamlingstelt kan opstilles jf. bilag 11 afsnit 2
Dokumentation udfærdiges af brandrådgiver certificeret til BK2
Dokumentation uden brug af certificeret brandrådgiver
Kommunal teknisk sagsbehandling af kap 5
Forsamlingstelt kan opstilles jf. certifikatet

2 ~~Transportable f~~Forsamlingstelte

Dette afsnit beskriver præ-accepterede løsninger til ~~transportable~~ forsamlingstelte, der opsættes midlertidigt, og omfatter kun telte, der ikke er opdelt i flere rum.

Forsamlingstelte er telte eller overdækninger med teltdug, der benyttes til dagopholdsfunktioner for flere end 50 personer og/eller er større end 50 m^2. Forsamlingstelte kan benyttes til midlertidig overnatning af højst 50 personer.

Afsnittet omhandler udelukkende forsamlingstelte i én etage, hvor de personer, der opholder sig i teltet, ikke nødvendigvis har kendskab til teltets flugtveje. Derudover er mindre telte til lagerformål på højst 50 m² og en brandbelastning på max. 800 MJ/m², der opsættes i forbindelse med forsamlingstelte, omfattet.

De forsamlingstelte der er omfattet af dette afsnit, vil typisk være:

- Cirkustelte.
- Telte til private eller offentligt tilgængelige fester for flere end 50 personer og/eller hvor teltet er større end 50 m^2.
- ~~Større og mindre s~~Salgstelte m.m. større end 100 m^2 på kræmmermarkeder m.m., hvor der er kundeadgang.
- Salgstelte pavilloner og lignende. på kræmmermarkeder m.m. beregnet til flere end 50 personer. Personer der er tilknyttet salgsteltet m.m. skal medregnes i personantallet.
- Telte der anvendes til restaurantlignende formål.
- Telte hvor der afholdes koncerter.
- Mastesejl.
- Bartelte.
- Køkkentelte med tilknytning til forsamlingstelte.

Følgende t~~T~~elte der ikke er omfattet af dette afsnit er:

- Telte der opsættes i mere end 6 uger (ikke midlertidigt)
- Salgsboder omfattet af afsnit 4:
  - Telte hvor der tilberedes og sælges mad fra, men hvor der ikke er ophold for kunder. ~~Disse betragtes om salgsboder.~~
  - Salgstelte m.m. på højst 100 m^2 på kræmmermarkeder m.m.
  - Salgstelte m.m. beregnet til højst 50 personer på kræmmermarkeder m.m. Personer der er tilknyttet salgsteltet m.m. skal medregnes i personantallet.

~~2.1~~

~~2.2~~2.1 Myndighedsbehandling

Inden et forsamlingstelt opstilles, skal det sikres, at det kan ske lovligt. For forsamlingstelte omfattet af dette bilag gælder følgende:

- Forsamlingstelte til privat formål kan opstilles uden byggetilladelse, hvis det er i 1 etage, jf. BR18 § 6-b, stk.1, nr. 1.
- Forsamlingstelt~~e~~, der ikke er til privat formål, kan opstilles uden byggetilladelse, hvis det er i 1 etage og har et areal på højst 100 m^2, jf. BR18 § 6-b, stk.1, nr. 2.
- Forsamlingstelt~~e~~ større end 100 m^2, der ikke er til privat formål, kan opstilles uden byggetilladelse, ~~hvis de har et areal på mere 100 m², og~~ hvis det er certificeret i henhold til bekendtgørelse om certificeringsordning for transportable konstruktioner og ikke anvendes til overnatning, jf. BR18 § 6-b, stk.2, nr. 2.
- For forsamlingstelt~~e~~, der ikke er undtaget for kravet om byggetilladelse jf. ovenstående, skal der ansøges om byggetilladelse, jf. BR18 § 10.

Med ændringsforslag i forhold til version 1.1

To eller flere forsamlingstelte der placeres med en indbyrdes afstand på mindre end 5,0 m betragtes som ét forsamlingstelt.

~~Hvis der skal søges byggetilladelse, skal dette ske via den digitale løsning som kommunen anvender.~~

~~2.2.1~~2.1.1 Meddelelse til kommunalbestyrelsen

For transportable konstruktioner, herunder forsamlingstelte, der anvendes af flere end 150 personer, skal meddelelse med oplysning om den transportable konstruktions indretning og brug, jf. §§ 156-158, sendes til kommunalbestyrelsen senest 4 uger før~~,~~ konstruktionen tages i brug jf. BR18 § 6e.

~~2.2.2~~2.1.2 Midlertidig o~~O~~vernatning i forsamlingstelte

Forsamlingstelte med et areal på højst 100 m^2 kan anvendes til midlertidig overnatning af højst 50 personer.

Der skal i forsamlingstelte, der anvendes til midlertidig overnatning opsættes mindst én røgalarm, som evt. er batteridreven.

Forsamlingstelte, der anvendes af forsvaret og redningsberedskabets, eller som anvendes i forbindelse med nødhjælpsarbejde, er ikke omfattet af retningslinjerne i dette bilag.

~~Hvis der ønskes overnatning i forsamlingstelte, skal det ske jf. bestemmelserne i BR18 § 152 aog kapitel 7 i denne vejledning.~~

~~Forsamlingstelte, der er certificerede, kan normalt opsættes uden byggetilladelse, hvis der ikke sker overnatning i teltet. Hvis det ønskes at overnatte i et forsamlingstelt, der er certificeret, vil det kræve en byggetilladelse.~~

~~2.3~~2.2 Indplacering i anvendelseskategorier, risikoklasser og brandklasser

~~Transportable f~~Forsamlingstelte, der ikke er undtaget for kravet om byggetilladelse, skal i henhold til BR18 §§ 84 og 490 indplaceres i anvendelseskategorier, risikoklasser og brandklasser.

Forsamlingstelte skal indplaceres i anvendelseskategori, risikoklasse og brandklasse på samme måde som forsamlingslokaler.

Typisk for forsamlingstelte er, at personer, der opholder sig i teltet~~:~~

- ikke nødvendigvis kender flugtvejene
- kan bringe sig selv i sikkerhed
- ikke overnatter i teltet.

Det betyder, at forsamlingstelte omfattet af dette bilag normalt kan henføres til:

- Anvendelseskategori 2, hvis personantallet højst er 50.
- Anvendelseskategori 3, hvis personantallet er større end 50.

Forsamlingstelte, der placeres med en indbyrdes afstand mindre end ~~10~~5,0 m, betragtes som ét telt i forbindelse med fastlæggelse af personantallet. Hvis der tilsammen i teltene er flere end 150 personer, skal der udarbejdes pladsfordelingsplaner.

Forsamlingstelte kan indplaceres i risiko- og brandklasser som angivet i Tabel 2 ~~Tabel 2-1~~, hvis de præ-accepterede løsninger i dette bilag følges i deres~~sin~~ helhed.

Med ændringsmarkeringer i forhold til version 1.1

Tabel 2-1 Sammenhæng mellem anvendelseskategori (AK), risikoklasse (RK) og brandklasse (BK).

	BK 1	BK 2	
	RK 1	RK 2	RK 3
AK 2	Brandmæssigt fritliggende bygninger med højst 1 etage over terræn, med et etageareal på højst 150 m^2, beregnet til højst ~~1~~50 personer, hvor der er direkte adgang til terræn i det fri fra alle opholdsrum~~.~~	Bygningsafsnit placeret i terrænniveau i højst 1 etage, ~~i bygninger med gulv i øverste etage højst 45,0 m over terræn~~ beregnet til højst 50 personer, hvor der er direkte adgang til terræn i det fri fra alle opholdsrum	
AK 3	Brandmæssigt fritliggende bygninger med højst 1 etage over terræn, med et etageareal på højst 150 m^2, beregnet til højst 150 personer, hvor der er direkte adgang til terræn i det fri fra alle opholdsrum.	Bygningsafsnit placeret i terrænniveau i højst 1 etage, ~~i bygninger med gulv i øverste etage højst 45,0 m over terræn,~~ hvor antallet af personer i bygningsafsnittet højst er 1.000	~~Bygningsafsnit placeret i terrænniveau i højst 2 etager, i bygninger hvor gulv i øverste etage er højst 45,0 m over terræn, og , hvor antallet af personer i bygningsafsnittet højst er 1.000~~

Hvis der opføres forsamlingstelte til ~~m~~flere end 1.000 personer, skal teltet indplaceres i risikoklasse 4, og dermed også i brandklasse 4, jf. BR 18 § 493, stk. 1 nr. 4.

Hvis et forsamlingstelt indplaceres i risikoklasse 2, og dermed brandklasse 2 ~~eller 3~~, kan~~og~~ der ~~af~~fraviges fra de præ-accepterede løsninger i dette bilag, jævnfør *BR18 Bilag 4 Fravigelser af de præ-accepterede løsninger i brandklasse 2 jf. § 493, stk. 1 nr. 2*. Ved flere fravigelser end angivet i bilag 4 skal~~vil~~ forsamlingsteltet ~~skulle~~ indplaceres i brandklasse 3 eller 4 jf. BR18 § 493, stk. 1 nr. 3 og 4.

I brandklasse 3 eller 4, jf. BR18 § 493, stk. 1, nr. 3 og 4 udføres dokumentationen som brandteknisk begrundet vurdering eller komparative analyse~~r~~ med udgangspunkt i de præ-accepterede løsninger, brandteknisk dimensionering, eller ved anvendelse af en kombination af metoderne, som beskrevet i denne vejlednings *Kapitel 8: Eftervisning*~~kapitel 8 i Bygningsreglementets vejledning til kapitel 5 – Brand~~.

~~2.4~~2.3 Certificeret brandrådgiver og statiker

Der er kun krav om indplacering i konstruktions- og brandklasser for forsamlingstelte, der kræver byggetilladelse, jf. BR18 § 493, stk. 2.

Forsamlingstelte, der er omfattet af krav~~et~~ om byggetilladelse, skal indplaceres i konstruktionsklasser, jf. BR18~~,~~ § 485, stk. 1. Hvis forsamlingsteltet indplaceres i konstruktionsklasse 2-4, kan der tilknyttes en certificeret statiker, der skal udfærdige dokumentationen for de bærende konstruktioner. Hvis der ikke tilknyttes en certificeret statiker, skal kommunalbestyrelsen foretage den tekniske sagsbehandling af dokumentationen af de bærende konstruktioner jf. BR 18 § 30-a.

Forsamlingstelte, der er omfattet af krav~~et~~ om byggetilladelse, skal indplaceres i brandklasser jf. BR18~~,~~ § 490, stk. 1. Hvis forsamlingsteltet indplaceres i brandklasse 2-4, kan der tilknyttes

Med forbehold for ændringer i forhold til høring version 1.1

en certificeret brandrådgiver, der skal udfærdige dokumentationen for brandforholdene. Hvis der ikke tilknyttes en certificeret brandrådgiver, skal kommunalbestyrelsen foretage den tekniske sagsbehandling af dokumentationen for brandforholdene jf. BR 18 § 31-a.

2.52.4 Teknisk sagsbehandling

Hvis der ikke inddrages en certificeret brandrådgiver eller statiker, skal kommunalbestyrelsen foretage teknisk sagsbehandling af de forhold, der vedrører brand og statik.

FraAfvigelser for retningslinjerne for redningsberedskabets indsatsmuligheder jf. afsnit 6, kræver ikke inddragelse af en certificeret brandrådgiver, men alene en tilladelse fra kommunalbestyrelsen, hvis forsamlingsteltet kræver byggetilladelse.

Det anbefales at afholde en forhåndsdialog med kommunalbestyrelsen især i de tilfælde, hvor der fraviges fra de indsatstaktiske forhold. Formålet med forhåndsdialogen er at drøfte de påtænkte løsninger og sætte det rette sikkerhedsniveau for de løsninger, der fraviger fra de indsatstaktisk traditionelle løsninger. Gennem dialog vil det være muligt, med kommunalbestyrelsens accept, at fravige de indsatstaktisk traditionelle løsninger, f.eks. baseret på lokale forhold.

2.62.5 Evakuering og redning af personer

2.6.12.5.1 Generelt

Det fremgår af BR18, § 91, at bygninger skal designes, projekteres og udføres, så der i tilfælde af brand kan ske en sikker evakuering og redning af personer. Det fremgår endvidere af § 91, at hovedformålet med kravet er, at evakuering og redning skal ske under hensyn til, at:

- 1) personer kan blive opmærksomme på, at der er opstået en brand.
- 2) flugtveje udformes, så der kan ske en evakuering af personer.
- 3) redningsåbninger udformes, så der kan ske redning af personer.

Præ-accepterede løsninger for brandtekniske installationer til varsling af personer er beskrevet i afsnit 2.7.1afsnit 2.7 i dette bilag.

2.6.22.5.2 Evakuering

Formålet med, at personer kan blive opmærksomme på, at en brand er opstået, er ifølge BR18, § 92, at der hurtigt kan påbegyndes en sikker evakuering. Dette skal ske under hensyn til:

1.1) Behov for tidlig detektering.
2.2) Behov for varsling af personer i bygninger.
3.3) Personers mulighed for og evne til ved egen hjælp at bringe sig i sikkerhed.
4.4) Behov for alarmering af redningsberedskabet.

Behov og mulighed for tidlig detektering er beskrevet i afsnit 2.7.1 i dette bilag.

2.6.32.5.3 Flugtveje herunder antal, udformning, sikring og sikring af brug

FEn flugtveje er i BR18, § 94 defineret som et sammenhængende system af udgange, gangarealer, flugtvejsgange og flugtvejstrapper, og den skal sikre, at personer kan forlade et forsamlingstelt på sikker vis.

Her angives funktionskrav, som fremgår af BR18 § 94, stk. 2, der skal sikre brug af flugtveje.

- Personers kendskab til flugtvejene i bygningen.
- At flugtveje skal være lette at identificere, nå og anvende.
- Personers mulighed for og evne til at anvende flugtveje i bygningen.
- At evakuering af personer på sikker vis kan ske til terræn i det fri eller til et sikkert sted i teltet og derfra på sikker vis til terræn i det fri.

Med anmærkninger fra udvalg til version 1.1

- ~~At der ikke opstår kritiske temperaturer, røgkoncentrationer, varmestråling eller tilsvarende kritiske forhold i det tidsrum, i hvilket flugtvejene skal anvendes til evakuering.~~
- ~~At flugtvejene skal være dimensioneret til det antal personer, der skal benytte dem~~
- ~~At døre i flugtveje skal være lette at åbne uden brug af nøgle og værktøj, og at døre i flugtveje, der skal anvendes af flere end 150 personer, skal åbne i flugtretningen.~~
- ~~At flugtveje skal være fri i hele den nødvendige bredde.~~

Som forudsætning for de præ-accepterede løsninger for udformning af flugtveje i dette afsnit gælder, at~~:~~

- U~~Der etableres mindst én udgang fra forsamlingsteltet, hvor en u~~dgang kan være en dør, en åbning eller anden mulighed for at komme ud af teltet på en let måde. Udgange skal føre direkte til terræn i det fri.
- E~~e~~vakuering af personer i formsamlingstelte sker som total evakuering. Herved forstås, at alle personer i forsamlingstelte forudsættes at påbegynde evakueringen samtidigt.
- A~~a~~lle udgange kan anvendes ved evakuering.

Da de præ-accepterede løsninger for forsamlingstelte kun omfatter telte, der ikke er opdelt i flere rum, vil evakuering af forsamlingstelt med inventaropstilling foregå via ~~flugtvejssystemet derfor sædvanligvis bestå af~~ flugtvejspassager, der fører fra opholdsområder til udgange til terræn i det fri. I flugtvejspassagerne kan der tillige være ramper og/eller trapper, der f.eks. betjener~~fører fra~~ tribuner eller indskudte etager.

2.5.4 Udgange

~~2.6.4~~2.5.4.1 *Antal udgange*

For at sikre, at personer ikke kan blive fanget i forsamlingsteltet i tilfælde af brand, skal der ~~som udgangspunkt~~ være følgende antal udgange:~~:~~

- ~~Forsamlingstelte på højst 150 m^2, der anvendes af højst 50 personer, skal have mindst en udgang direkte til terræn i det fri.~~
- ~~Forsamlingstelte større end 150 m^2 til højst 50 personer, skal have mindst to udgange direkte til terræn i det fri.~~
- Forsamlingstelte der anvendes af fl~~m~~ere end 50 personer og højst ~~af~~ 150 personer, skal have mindst to udgange direkte til terræn i det fri.
- Forsamlingstelte til fl~~m~~ere end 150 personer skal have mindst tre udgange direkte til terræn i det fri, og den samlede bredde af udgangene skal svare til mindst 10 m ~~c~~m pr. person. Den samlede bredde på udgangene skal fordeles jævnt på antallet af udgange.
  Der bør ~~t anbefales, at der~~ etableres yderligere en udgang, hver gang personantallet øges med 200 ~~personer.~~
- Telte der anvendes som køkkentelte hvor der produceres mad m.m., skal have mindst to udgange direkte til terræn i det fri, uanset teltets størrelse og personbelastning.

I forsamlingstelte, hvor der er betinget mere end en udgang, skal udgangene placeres i modstående~~satrettede~~ ender, og afstandene mellem udgangene skal være mindst 5,0 m.

~~2.6.5~~2.5.5 Udformning af udgange

For at en udgang kan udlægges som flugtvej, skal den tydeligt fremtræde som udgang, og den skal let kunne passeres uden brug af nøgle eller ~~særligt~~ værktøj.

For forsamlingstelte indrettet til flere end 150 personer skal der jf. BR18 § 96, stk. 1, nr. 2 installeres flugtvejs- og panikbelysning. Se dog afsnit 2.7.2 vedrørende særlige forhold til flugtvejs- og panikbelysning for forsamlingstelte.~~Over eller umiddelbart ved udgangen skal der~~

Med ændringsforslag i forhold til version 2.1

~~anbringes flugtvejsskilte udført i overensstemmelse med Arbejdstilsynets Bekendtgørelsen nr. 518 af 17. juni 1994 med senere ændringer om sikkerhedsskiltning og anden form for signalgivning~~

For at sikre, at de personer, der opholder sig i forsamlingsteltet, kan komme hurtigt ud af teltet, skal det sikres, at udgange i telte til højst 150 personer~~,~~ har en bredde på mindst 0,77 -m, og i forsamlingstelte til fl~~m~~ere end 150 personer, skal det sikres, at udgangene har en bredde på mindst 1,2 m.

Udgange, der ikke anvendes i den normale drift af teltet, vil typisk være lukket med lynlåse. Dette kan accepteres, såfremt lynlåsen er funktionsduelig og letløbende, og at der ved udgangen findes en afmærkning, der viser, hvor lynlåsen er placeret, og i hvilken retning den løber f.eks. som vist på nedenstående figur~~Figur 2-1~~.



Figur 2-1 Mærkning af udgang og lynlås.

En anden mulighed er at benytte en lukning med velcrobånd f.eks. som vist på nedenstående figur~~Figur 2-2~~. Her er det vigtigt, at velcrobåndet er let at åbne, så ~~ledes at~~ flugtvejen er let at passere.



Figur 2-2 Udgang med velcrobånd.

Endelig kan der også anvendes gående døre. Kravet til dørene~~s~~ er de samme som til de øvrige udgange, og det skal derudover sikres, at dørene åbner i flugtvejsretningen, hvis forsamlingsteltet anvendes af flere end 150 personer.

~~2.6.6~~2.5.6 ~~Udformning af p~~Pladsfordelingsplaner

Ved forsamlingstelte, der ~~skal~~ benyttes af fl~~m~~ere end 150 personer, skal der jf. BR18 § 157, nr. 1, udarbejdes en pladsfordelingsplan, der viser inventaropstilling samt flugtveje til terræn i det fri.

Pladsfordelingsplaner, som ikke er en del af en certificering af en transportabel konstruktion, skal udfærdiges af en certificeret brandrådgiver eller indgå i forbindelse med ansøgning om byggetilladelse ~~og godkendes af kommunalbestyrelsen~~, jf. BR18 § 6h.

Hvis forsamlingsteltet anvendes uden inventaropstilling, skal der ophænges et opslag med det ~~største~~ højeste antal personer, der må opholde sig i teltet.

Såfremt forsamlingsteltet ændrer udformning, eller hvis inventaropstillingen ændres, skal der udarbejdes en ny pladsfordelingsplan.

~~Dette kan ske gennem certificeringsorganet, der har certificeret forsamlingsteltet, eller den kan udfærdiges af en certificeret brandrådgiver, eller godkendes af kommunalbestyrelsen.~~

Alle opslag eller pladsfordelingsplaner skal udføres i plant holdbart materiale og ophænges på et tydeligt, let læseligt sted ved alle primære indgange ~~udført i plant holdbart materiale~~.

Udarbejdelse af pladsfordelingsplaner er nærmere beskrevet i~~:~~

- Bygningsreglementets vejledning til kapitel 29 - Dokumentation af brandforhold.
- Bilag 13 i denne vejledning.
- Bilag 11c i denne vejledning.

Hvor der anvendes tribuner og~~,~~ scener m.v. i et telt, skal flugtvejsforhold og placering af disse fremgå af teltets pladsfordelingsplan~~en for teltet~~.

Med ændringsmarkeringer i forhold til version 1.1

~~2.7~~2.6 Antændelse, brand og røgspredning

~~2.7.1~~2.6.1 Generelt

Det fremgår af BR18 § 104, at byggeri skal projekteres og udføres, så det sikres, at der i tilfælde af brand ikke sker væsentlig brand- og røgspredning. Dette skal ske under hensyn til, at~~:~~

~~1.~~1) R~~r~~isikoen for, at en brand opstår, begrænses.
~~2.~~2) B~~b~~rand- og røgspredning begrænses i den brandmæssige enhed, hvor branden er opstået.
~~3.~~3) B~~b~~rand- og røgspredning til andre brandmæssige enheder forhindres i den tid, som er nødvendig for evakuering og redningsberedskabets indsats.
~~4.~~4) B~~b~~randspredning til bygninger på samme grund begrænses.
~~5.~~5) D~~d~~er ikke sker brandspredning til bygninger på anden grund.

Præ-accepterede løsninger for brandtekniske installationer til begrænsning af brand- og røgspredning er beskrevet i afsnit *2.7* ~~i dette bilag~~.

~~2.7.2~~2.6.2 Placering af forsamlingstelte

Det fremgår af BR18 § 118 og § 125, at byggeri skal placeres i en sådan afstand til hinanden og til skel mod nabo, vej- og stimidte eller udføres på en sådan måde, at det sikres, at der ikke er risiko for brandspredning mellem bygninger på samme grund eller til anden grund.

Forsamlingstelte opstilles oftest steder, hvor det ikke er muligt at overholde afstande til naboskel, vej- eller stimidte. Derfor vil afstandskrav for forsamlingstelte enten være en afstand til skel (nabo-, vej- og stiskel) eller et krav til en indbyrdes afstand mellem forsamlingsteltet og andre elementer.

Det skal sikres at forsamlingsteltet ~~enten:~~

- placeres mindst 5,0 m fra skel

og/eller

- at afstanden fra forsamlingstelte til eksempelvis salgsområder, campingområder, bygninger, brandfarlige oplag m.v., har en indbyrdes afstand, der mindst svarer til summen af de afstande, de hver især skal have til naboskel.

Afstande måles vandret uden hensyn til ~~terræn~~forskelle i terrænniveau. Afstanden er den mindste frie afstand mellem et forsamlingstelt og et skel eller en bygning. Afstande til forsamlingstelte måles som afstanden til teltdugen.

Ved placeringen af forsamlingstelte, ~~skal der være opmærksom på, at~~må teltet ikke hindre~~r~~ brug af udgange fra forsamlingsteltet eller fra bygninger som forsamlingsteltet placeres i nærheden af. Ved placering af teltet skal det ~~tillige~~ også sikres, at redningsberedskabets indsatsmuligheder ikke forringes, dvs. at teltet ikke placeres på udlagte brandveje, eller placeres, så redningsarealer eller lign. ikke kan anvendes. Dette omfatter også barduner til telte.

For certificerede forsamlingstelte, der ikke kræver byggetilladelse, kan der være forhold i certificeringen, der skal iagttages i forbindelse med placering af teltet. Forhold, der relaterer sig hertil, skal fremgå af ~~inspektionsrapporten~~certifikatet, og bør desuden fremgå af opstillingsvejledningen for teltet, så det placeres korrekt på grunden. Hvis forsamlingsteltet ikke opføres med den afstand, der er angivet i certifikatet, kræves der derfor en byggetilladelse.

Med ændringsmarkeringer i forhold til version 1.1

~~Konkrete afstandskrav skal ikke fremgå af certifikatet, da placeringen af konstruktionen ikke kendes på certificeringstidspunktet. Det er altså alene krav, der relaterer sig til den konkrete konstruktion, der skal fremgå af certifikatet.~~

To eller flere forsamlingstelte der placeres med en indbyrdes afstand på mindre end 5~~10~~,0 m betragtes som ét forsamlingstelt. Hvis der i certifikatet er angivet større indbyrdes afstand end 5,0 m, ~~så~~ er det certifikatets afstandskrav, der er gældende.

Eksempler på indbyrdes afstande:

- En bygning med beton eller murstensfacade skal normalt holdes en afstand på 2,5 m fra naboskel. Det betyder, at afstanden mellem forsamlingstelt~~et~~ og bygning skal være 5,0 m + 2,5 m = 7,5 m.
- Et salgsområde skal normalt holde en afstand på 5,0 m til naboskel. Det betyder, at afstanden mellem et forsamlingstelt og salgsområde skal være 5,0 m + 5,0 m = 10,0 m.
- En bygning med et stråtag skal normalt holdes 10,0 m fra naboskel. Det betyder, at afstanden mellem forsamlingsteltet og bygningen med stråtag skal være 5,0 m + 10,0 m = 15,0 m.

Afstanden til ~~mindre bygninger~~sekundære bebyggelser på højst 50 m^2, ~~som~~ f.eks. garager, carporte, udhuse og lignende skal være mindst 5,0 m.

~~2.7.3~~2.6.3 Indvendige og udvendige overflader

Indvendige overflader skal ifølge BR18~~,~~ § 109 designes, projekteres og udføres, så de ikke bidrager væsentligt til brand- og røgspredning som følge af de indvendige overfladers brandtekniske egenskaber:

- Antændelighed
- Brandspredning
- Produktion af varme og røg
- Produktion af brændende dråber og partikler.

Teltdug~~en~~ i forsamlingstelte skal derfor udføres af 1 lags teltdug ~~materialer~~, der ikke bidrager til en brand.

Da de indvendige og udvendige overflader udgøres af teltdugen, er krav til ~~de~~ ind- og udvendige overflader ~~de samme~~ens.

Teltdug~~en~~ til forsamlingstelte til fl~~m~~ere end 150 personer, skal udføres af et brandmæssigt egnet materiale. Det~~te~~ skal~~kan~~ dokumenteres efter en af følgende standarder:

- SIS 65 00 82 Bestämning av brandhärdighet hos vävnader~~.~~
- T1 produkt i henhold til DS/EN 15619 Gummi- eller plastbelagte stoffer - Midlertidige konstruktioner (telte) - Sikkerhed - Specifikation af belagte stoffer til telte og lignende konstruktioner~~.~~
- DS/EN 14115 Textiler - Brandforhold, større telte og lignende produkter – Antændelighed.

~~2.7.4~~2.6.4 Risiko for antændelse

Installationer og andre tiltag, som kan medføre en særlig risiko for, at en brand opstår, ~~udføres~~skal ifølge BR18 § 105~~, i bygningen,~~placeres og udføres så risikoen for, at en brand opstår og spreder sig, minimeres.

Med ændringsmarkeringer i forhold til version 1.1

Det skal derfor sikres, at risikoen for antændelse af en brand i forsamlingstelte begrænses.

~~2.7.4.1~~2.6.4.1 *Rumopvarmning*

Opvarmning af forsamlingstelte, som placeres i forsamlingsteltet, skal ske med elvarme eller med gasfyrede ~~aggregat~~apparater med direkte fordampning.

Der skal holdes en afstand fra varmeapparater til antændelige materialer i henhold til produktets anvisninger.

Øvrige olie- eller gasfyrede ~~aggregater~~apparater til rumopvarmning, der ikke er placeret i forsamlingsteltet, skal være anbragt mindst 5,0 m fra forsamlingsteltet

~~2.7.4.2~~2.6.4.2 *Elektriske ~~Tekniske~~ Installationer*

Elektriske installationer skal opfylde bestemmelserne i Installationsbekendtgørelsen ~~og den underliggende standard serie *DS/HD 60364-serien*~~.

~~2.7.4.3~~2.6.4.3 *F-gas*

Gasinstallationer skal opfylde bestemmelserne i gasreglementet udstedt af Sikkerhedsstyrelsen. Gyldig gasinstallations-attest skal forefindes, og den autoriserede virksomhed skal anbringe mærkater på apparaterne, når de er blevet kontrolleret.

Der må i ~~et~~ forsamlingstelte til højst 150 personer højst anbringes 5 stk. F-gas~~installationer~~anlæg, herunder kogeapparater m.v., transportable varmeovne til F-gas, inkl. de F-gasflasker, der aktuelt er i brug. Alle øvrige F-gasflasker, herunder reserveflasker, skal anbringes i overensstemmelse med de for oplag gældende bestemmelser i Beredskabsstyrelsens tekniske forskrifter for gasser.

Anlæg af brandfarlige gasser (Gas eller gasblanding, der er antændelig i atmosfærisk luft) må ikke etableres i forsamlingstelte til flere end 150 personer.

Forsamlingstelte og lagerafsnit med brandfarlige gasser skal have en indbyrdes afstand af mindst ~~5~~10,0 m.

~~Alle øvrige F-gasflasker, herunder reserveflasker, skal anbringes i overensstemmelse med de for oplag gældende bestemmelser i Beredskabsstyrelsens tekniske forskrifter for gasser.~~

~~2.7.4.4~~2.6.4.4 *Oplag m.v.*

Der må ikke placeres oplag i forsamlingstelte til fl~~m~~ere end 150 personer, hvis oplaget er omfattet af Beredskabsstyrelsens tekniske forskrifter, eller oplag, der medfører, at der i forsamlingsteltet er en brandbelastning større end 800 MJ/m^2 gulvareal.

Derudover må der ikke være større mængder af halm, træ og lignede, ligesom der ikke må opstilles affaldscontainere m.v. med et rumfang over 1 m^3.

Større mængder brandfarligt oplag såsom halm, brandfarlig emballage og affald, der placeres uden for et forsamlingstelt~~e~~, kan udgøre en risiko for brandspredning og ~~bør~~ skal ~~hermed~~ placeres i en afstand på mindst 10,0 m fra forsamlingstelte~~t~~.

Krav til afstand mod naboskel for oplag af drivmidler, f.eks. benzin, dieselolie og andre flydende brændstoffer, fremgår af Beredskabsstyrelsens tekniske forskrifter for brandbare og brandfarlige væsker.

~~2.8~~2.7 Brandtekniske installationer i forsamlingstelte

I BR18 §§ 88-90 er de overordnede krav til brandtekniske installationer beskrevet. Af BR18 § 88 fremgår, hvilke formål brandtekniske installationer kan bidrage til~~,~~ ved brandsikring af bygninger, og af BR18 § 90 fremgår en række krav til, hvor~~ledes~~dan brandtekniske installationer og slukningsmateriel skal projekteres og installeres i bygninger.

Med ændringsmarkeringer for høring til version 1.1

Efterfølgende angives i BR18 §§ 91-133 en række detaljerede krav til, hvilke brandtekniske installationer, der skal installeres i en bygning afhængigt af bygningsafsnittets anvendelseskategori og risikoklasse.

Af BR18~~,~~ § 89 fremgår det, at brandkrav til brandtekniske installationer i BR18 §§ 90-133 kan fraviges, hvis det dokumenteres, at kravene i BR18 § 82 opfyldes på anden vis. I dette bilag er det angivet, hvilke brandtekniske installationer, der kan fravige kravene i BR18 §§ 90-133, samt hvilke brandtekniske foranstaltninger, der skal erstatte fravigelserne.

Transportable konstruktioner, herunder forsamlingstelte, er undtaget for, at der skal foretages akkrediteret funktionsafprøvning~~er~~ af de brandtekniske installationer som beskrevet jf. BR18 §~~§ 134 og~~ 141, stk. 5~~1~~.

Drift af de brandtekniske installationer skal ske i henhold til bestemmelserne i BR18 §§ 141-142.

Det forudsættes endvidere, at alle brandtekniske installationer designes, projekteres, udføres og kontrolleres som angivet i denne vejlednings *B ~~b~~ilag 12: ~~i denne vejledning~~ Præ-accepterede løsninger for brandtekniske installationer og håndslukningsudstyr*.

~~2.8.1~~2.7.1 Varsling

I forsamlingstelte til fl~~m~~ere end 150 personer, herunder bl.a. cirkustelte, der opstilles ~~midlertidigt~~ i op til 6 uger, er der, jf. § 93, stk. 3, ikke krav om at der installeres et varslingsanlæg, såfremt det dokumenteres, at der kan foretages en anden tilstrækkelig varsling af personer.

Varslingen kan f.eks. foregå via det generelle lydanlæg bemandet af personalet, eller ved at personalet umiddelbart har adgang til megafoner, og der er udarbejdet en instruks for ~~denne~~ varsling, herunder intern kommunikation til personalet om, hvordan varsling~~en~~ iværksættes.

Det skal dog tydeligt fremgå af brand- og evakueringsinstruksen, hvordan den konkrete varsling af teltet skal foregå, så den er entydig for de personer, der opholder sig i forsamlingsteltet.

~~2.8.2~~2.7.2 Flugtvejs- og panikbelysning

For forsamlingstelte indrettet til flere end 150 personer skal der installeres flugtvejs- og panikbelysning jf. ~~, fremgår det af~~ BR18 § 96, stk. 1, nr. 2~~ og 3, at der skal installeres flugtvejsbelysning ved udgangene og panikbelysning i de flugtvejspassager, der fører til udgangene~~.

Hvor telte ikke anvendes efter mørkets frembrud, og teltets materialer og udformning ikke udelukker en rimelig dagslysmængde, kan belysning af flugtvejsskilte og panikbelysning udelades.

Placering og udførelse af flugtvejs- og panikbelysning skal ske ved at følge retningslinjerne i denne vejlednings *Bilag 12: Præ-accepterede løsninger for brandtekniske installationer og håndslukningsudstyr.*

~~2.8.3 fra bilag 12 i denne vejledning.~~

~~2.8.4~~2.7.3 Brandslukningsudstyr

I forsamlingstelte med et etageareal større end 1.000 m^2 eller til flere end 150 personer skal der opstilles brandslukningsmateriel, så der kan foretages en indledende slukning.

For traditionelle forsamlingstelte, der er omfattet af dette bilag, er det tilstrækkeligt, at der placeres trykvandslukkere eller håndsprøjtebatterier~~ eller trykvandslukkere~~, så der højst er 30 m i ganglængde til det nærmeste slukningsudstyr.

Med ændringsbemærkninger i forhold til Version 1.1

I forsamlingstelte til flere end 150 personer skal der uUd over trykvandslukkere og håndsprøjtebatterier ~~skal der, i forsamlingstelte til flere end 150 personer,~~ opsættes kulsyreslukker ved el-tavler, mikserpulte og lignende særlige elektriske installationer.

Håndslukningsudstyr skal anbringes synligt og være let tilgængeligt og skal om muligt placeres ved teltets udgange.

Håndslukningsudstyr skal opsættes og følge beskrivelserne i denne vejlednings *Bilag 12: Præ-accepterede løsninger for brandtekniske installationer og håndslukningsudstyr.* ~~bilag 12 i denne vejledning~~.

~~2.8.5~~2.7.4 Automatisk sprinkleranlæg

I henhold til BR18 § 123, stk. 2, er telte med en brandbelastning på højst 800 MJ/m^2 undtaget for installation af automatisk sprinkleranlæg. Da dette bilag kun omfatter forsamlingstelte med en brandbelastning på højst 800 MJ/m^2, jf. afsnit ~~afsnit~~ *2.6.4.4*, er d~~e~~isse undtaget for installation af automatisk sprinkleranlæg.

~~2.9~~2.8 Brandmodstandsevne for bærende konstruktioner

~~2.9.1 Generelt~~

~~Det fremgår af BR18 § 99, at bygninger og bygningsdele skal have en tilstrækkelig brandmodstandsevne. Projektering og udførsel af bygningers konstruktioner skal ske under hensyn til, at:~~

1. ~~Evakuering af de personer, der opholder sig i bygningen, kan ske på sikker vis, og at der ikke sker væsentlige skader på bygningen.~~
2. ~~Der ikke sker skade på personer og bygninger på anden grund.~~
3. ~~Redningsberedskabet har forsvarlig mulighed for redning af personer og for at gennemføre det slukningsarbejde og den begrænsning af brandspredning, som er nødvendig herfor.~~
4. ~~Der ikke sker væsentlige skader på andre bygninger på egen grund, som kan medføre fare for personer eller redningsberedskabets indsatsmulighed.~~

~~2.9.2~~2.8.1 Brandmodstandsevne

Telte adskiller sig fra traditionelle bygninger ved at være langt mere utætte end traditionelle bygninger, ligesom teltdugen vil smelte væk inden der opstår kritiske forhold for de bærende konstruktioner. Dette kan sidestilles med en bygning med automatisk brandventilation, hvor der ikke er krav til ~~brandmodstandsevnen af~~ de bærende konstruktioner~~s~~ brandmodstandsevne.

Bærende konstruktioner kan derfor udføres uden krav til brandmodstandsevne, også selvom den enkelte bærende konstruktion bærer mere end 200 m^2.

~~2.10~~2.9 Ordensregler for forsamlingstelte

Ved forsamlingstelte til ~~m~~flere end 150 personer, skal det af hensyn til brandsikkerheden sikres, at~~:~~

- O~~o~~mrådet inden for 5,0 m fra forsamlingstelte ikke anvendes til parkering ~~og lignende~~ af motordrevne køretøjer, herunder eldrevne køretøjer. Af- og pålæsning er dog tilladt.
- B~~b~~orde- og bænkesæt og lign. der opsættes uden for teltet ikke indskrænker flugtvejenes frie bredde helt til det fri
- D~~d~~er ved udgange ikke parkeres motorkøretøjer, cykler m.v.
- D~~d~~er ikke er oplag, beplantning eller lignende, som kan hindre evakuering.
- D~~d~~en frie bredde af gangarealer uden for forsamlingsteltet ikke indskrænkes af master, tælleapparater, barduner, projektører m.v.

Medarbejdermarkering til høring til version 1.1

-
- ~~Større mængder af l~~Letantændelig vegetation fjernes inden for 10,0 m fra forsamlingstelte.
-

Med ændringsmarkeringer i forhold til version 1.1

3 Midlertidige ~~udendørs~~ campingområder

Dette afsnit beskriver præ-accepterede løsninger for midlertidige campingområder til flere end 150 personer, der ikke er omfattet af campingreglementet~~, til flere end 150 personer~~.

Et campingområde er et samlet sammenhængende område i det fri, hvor der opstilles telte, campingvogne og lignende campingenheder.

Telte i dette afsnit er campingtelte til overnatning på højst 50 m^2 og/eller beregnet til højst 50 personer.

I campingområder, hvor der placeres oplag, der er omfattet af Beredskabslovgivningen, skal oplagene indrettes og placeres efter detailkravene i Beredskabslovningens bekendtgørelser. ~~Eksempler på~~ Oo~~p~~lag, der kan være omfattet af Beredskabslovgivningen indeholder eksempelvis ~~er oplag bestående af~~ gasser, brandfarlige væsker eller større oplag af brandfarlige faste stoffer.

3.1 Myndighedsbehandling

3.1.1 Campingområder til højst 150 personer

Campingområder til højst 150 personer er ikke omfattet af Bygningsreglementet, jf. BR18 § 4, nr. 7). Personantallet bestemmes som det forventede største~~maksimale~~ antal personer, der vil være på campingområdet samtidigt. Personer, der er tilknyttet arrangementet m.m., skal medregnes i personantallet.

Der er derfor ikke krav til indretning af campingområder til højst 150 personer.

3.1.2 Campingområder til flere end 150 personer

Campingområder til flere end 150 personer skal overholde Bygningsreglementets krav i kapitel 5 - B~~b~~rand. Personantallet bestemmes som det forventede største~~maksimale~~ antal personer, der vil være på campingområdet samtidigt. Personer, der er tilknyttet arrangementet m.m., skal medregnes i personantallet.

Hvis de præ-accepterede løsninger i dette bilag følges deres~~i sin~~ helhed, anses ~~vil~~ brandkravene i *Bygningsreglementets kapitel 5 – B~~b~~rand* for ~~som udgangspunkt~~ værende overholdt.

3.1.2.1 Byggetilladelse

Campingområder til flere end 150 personer, der følger de præ-accepterede løsninger i dette bilag som helhed, kan jf. BR18 § 6-f, stk. 2, etableres uden ansøgning om byggetilladelse, uanset personantal og areal af campingområdet.

Hvis de præ-accepterede løsninger i dette bilag ikke følges i deres~~sin~~ helhed, skal der ansøges om byggetilladelse, og ~~skal~~ kommunalbestyrelsen skal meddele byggetilladelse, inden campingområdet må etableres.

3.1.2.2 Meddelelse til kommunalbestyrelsen

Jf. § 6-f, ~~S~~stk. 3. skal kommunalbestyrelsen have meddelelse om etablering af campingområde ~~der~~ for campingområder til flere end 150 personer ~~ske meddelelse til kommunalbestyrelsen om etableringen af campingområdet~~. Meddelelsen skal indeholde oplysninger om campingområdets placering, indretning og brug, jf. *Bygningsreglementets kapitel 5 - Brand*. Meddelelsen skal være modtaget af kommunalbestyrelsen senest 4 uger før~~,~~ området tages i brug.

Oplysning om campingområdets placering, indretning og brug sker ved at udarbejde en arrangementsplan over området. Planen ~~skal i nødvendigt omfang~~ bør suppleres med en kort beskrivelse af brugen af området.

Med andre mark-ringer i forhold til version 1.1

Meddelelse til kommunalbestyrelsen skal ske~~,~~ uanset om etableringen af campingområdet kræver byggetilladelse eller ej.

Det skal bemærkes, at de 4 uger ikke er et servicemål for kommunalbestyrelsen, og i de tilfælde, hvor der kræves en byggetilladelse, kan sagsbehandlingstiden ~~godt længere end de~~overstige 4 uger. Ansøger bør derfor på forhånd orientere sig i kommunens sagsbehandlingstid for byggesager og indsende ansøgningen i overensstemmelse hermed. Tidsfristen er ~~alene givet, så det~~kun angivet for at sikre~~s~~, at kommunalbestyrelsen og redningsberedskabet har mulighed for at planlægge eventuel~~t~~le tilsyn.

3.1.2.3 *Teknisk byggesagsbehandling*

I BR18 § 6-f, stk. 4 beskrives det, at hvis det vurderes, at der skal inddrages en certificeret brandrådgiver, kan ansøger i stedet vælge, at kommunalbestyrelsen ~~i stedet~~ skal foretage teknisk byggesagsbehandling af ~~afvigelserne fra de præ-accepterede løsninger~~ brandforhold jf. *Bygningsreglementets kapitel 5 – Brand*~~. Den kommunale sagsbehandling skal dog kun omfatte afvigelser fra de præ-accepterede løsninger på baggrund af den dokumentation som ansøger fremsender~~.

3.1.2.4 *Certificeret statiker og brandrådgiver*

Campingområder er undtaget fra indplacering i konstruktionsklasser jf. BR18 § 489, stk. 3. Det er dog kun indretning af områderne som helhed, der er undtaget, og ikke eventuelle telte eller andre transportable konstruktioner, der placeres i områderne. Hvis der er telte eller andre transportable konstruktioner, der ikke er certificerede og som kræver byggetilladelse, skal der enten anvendes en certificeret statiker eller foretages kommunal teknisk sagsbehandling.

Campingområder er undtaget fra indplacering i brandklasser jf. BR18 § 493, stk. 3. Det er dog kun indretning af områderne som helhed, der er undtaget, og ikke eventuelle telte eller andre transportable konstruktioner, der placeres i områderne. Det skal dog i hvert tilfælde vurderes om der skal inddrages en certificeret brandrådgiver, og i hvor stort omfang, der skal udarbejdes dokumentation. Denne vurdering foretages af kommunalbestyrelsen.

For campingområder skal der ikke inddrages en certificeret brandrådgiver, hvis områderne udformes og indrettes efter de præ-accepterede løsninger i dette bilag i sin helhed.

Hvis ~~der fraviges fra~~ de præ-accepterede løsninger i dette bilag fraviges, skal det på anden vis dokumenteres, at *Bygningsreglementets kapitel 5 – Brand* er overholdt. ~~Denne D~~dokumentationen ~~skal~~kan udfærdiges af en certificeret brandrådgiver~~, der skal være certificeret til mindst brandklasse 2~~. Alternativt kan ~~, og have kvalifikationerne til at kunne vurdere fravigelserne~~ ansøger vælge, at kommunalbestyrelsen skal foretage teknisk sagsbehandling af fravigelserne fra de præ-accepterede løsninger af brandforhold jf. *Bygningsreglementets vejledning til kapitel 5 – Brand*. Omfanget af dokumentationen begrænser sig ~~alene~~ til fravigelserne~~, og der skal ikke udarbejdes start- og sluterklæring~~.

~~Af~~Fravigelser for de præ-accepterede løsninger for redningsberedskabet indsatsmuligheder kræver ikke inddragelse af en certificeret brandrådgiver, men ~~alene en~~ kun tilladelse fra kommunalbestyrelsen.

3.2 Indretning af campingområder

Indretning af campingområder skal ske, så det sikres, at ~~de~~ personer, der opholder sig i campingområder, kan komme væk~~evakuere~~ fra området og~~, samt at~~ der ikke kan ske~~r~~ væsentlig brandspredning. ~~Ligeledes~~ Det skal ~~det~~ også sikres, at redningsberedskabet har mulighed for at foretage en sikker indsats. Campingområder skal indrettes, så risikoen for brandspredning mellem campingenhederne mindskes mest muligt. For at sikre dette, skal campingområder inddeles i:~~:~~

Med forbehold for politisk godkendelse i forhold til version 1.1

- Teltområder ~~med mindre telte.~~
- ~~Teltområder med større telte.~~
- Caravanområder~~.~~
- Blandede områder.

Det skal derudover sikres, at campingområder placeres mindst 5,0 m fra skel, eller at afstanden fra campingområder til eksempelvis forsamlingstelte, salgsområder, bygninger, brandfarlige oplag m.v., skal have en afstand, der mindst svarer til summen af de afstande, de hver især skal have til naboskel. Eksempler på indbyrdes afstande:

- En bygning med beton eller murstensfacade skal normalt holde~~s i~~ en afstand på 2,5 m fra naboskel. Det betyder at afstanden mellem campingområde og bygning skal være 5,0 m + 2,5 m = 7,5 m.
- Et forsamlingstelt skal normalt holde en afstand på 5,0 m til naboskel. Det betyder, at afstanden mellem campingområde og forsamlingstelt skal være 5,0 m + 5,0 m = 10,0 m.
- En bygning med ~~et~~ stråtag skal normalt holde~~s~~ en afstand på 10,0 m ~~fra~~ til naboskel. Det betyder, at afstanden mellem campingområde og bygning skal være 10,0 m + 5,0 m = 15,0 m.

3.2.1 Teltområder

Teltområder skal inddeles i felter af højst 3.000 m^2.

I teltområder skal den indbyrdes afstand mellem teltene være mindst 3,0 m. Afstanden måles fra teltdug til teltdug.

Rundt om felter i teltområder skal der være et friområde med en bredde på mindst:

- 5,0 m hvis feltet er højst 1.000 m^2.
- 7,0 m hvis feltet er højst 2.000 m^2.
- 10,0 m hvis feltet er højst 3.000 m^2.
- 10,0 m for teltområder med flere felter, der samlet har et areal på mere end 20.000 m^2.

Ved beregning af teltområders areal medtages friområder ikke.

Den indbyrdes afstand mellem mindre telte på højst 9 m^2 kan fraviges hvis:

- Telte inden for et felt opstilles i klynger af 8 telte, og hvis der mellem klyngerne er et friområde på mindst 2,0 m regnet fra bardun til bardun

eller

- Telte opstilles i felter på højst 500 m^2 med friområder på mindst 5,0 m

3.2.2 Caravanområder

Caravanområder er områder, hvor der opstilles campingvogne, campletter, autocampere og lignende.

Caravanområderne skal opdeles i felter på højst 500 m^2, og der skal rundt om hvert felt være et friområde på mindst 5,0 m.

I et caravanområde kan en campingenhed bestå af eksempelvis en campingvogn og et mindre telt svarende til et iglotelt eller lignende~~.~~ ~~med dimensioner på 3 m x 3 m x 2 m (l x b x h)~~på højst 9,0 m^2.

Eventuelle overdækninger, solsejl, markiser eller lignende~~.~~, der opsættes som en fast del af campingenheden, skal medregnes, når afstandskravet ~~skal~~ måles.

Med ændringsmarkeringer i forhold til version 1.1

I caravanområder skal den indbyrdes afstand mellem campingenhederne være mindst 3,0 m. Den indbyrdes afstand regnes fra den samlede campingenhed. Afstanden måles fra campingvognskasse, fortelte, mindre telte eller lignende~~.~~, ~~hvorimod~~ mens trækstænger ikke medregnes.

3.2.3 Blandede områder

Blandede områder kan bestå af campingenheder, der udgøres af caravans og telte.

Blandede områder skal opdeles i felter på højst 500 m^2 og der skal rundt om hvert felt være et friområde på mindst 5,0 m.

I blandede områder skal den indbyrdes afstand mellem campingenhederne være mindst 3,0 ~~-~~m.

I blandede områder kan campingenheder bestå af eksempelvis en campingvogn og et mindre telt, eller et større telt og et mindre telt. Den indbyrdes afstand regnes fra den samlede campingenhed. Et mindre telt defineres som højst 9 m^2.

3.3 Udarbejdelse af plan~~tegninger~~ for campingområder

~~Hvis d~~Der skal udarbejdes en målfast ~~situations~~plan, der viser placering, indretning og brug af campingområdet. Planen bør ~~den~~ mindst angive~~vise~~ følgende:

- Størrelse og placering af felter med telt-, caravan- og blandede områder.
- Friområder, herunder friområder, der anvendes til evakuering~~flugtveje~~. Det skal fremgå hvor brede friområderne er.
- Brandslukningsmateriel.
- Placering af områder, hvor der må anvendes grill~~er~~, bålfad~~e~~ og bål.
- Affaldsbeholdere.~~—~~
- Udgange og flugtvejsmulighedere~~.~~

I campingområder kan ~~udgøres evakueringflugtveje af~~ de friområder, der udlægges mellem de enkelte felter benyttes til evakuering. I ~~felter uden krav til afstand mellem mindre telte~~ teltområder, caravanområder og blandede områder må der ~~intet sted~~aldrig være en ganglængde på mere end 30 m til nærmeste friområde.

~~Ved arrangementer der omfatter forsamlingstelte, camping- og salgsområder, og eventuelt andre områder, der ikke er omfattet af dette bilag, såsom koncertområder foran scener, forlystelser, parkeringsarealer m.m. skal der udarbejdes en arrangementsplan, der giver et samlet overblik over de enkelte områder, og redningsberedskabets muligheder for at kunne komme frem på området.~~

~~Arrangementsplanen er en del af den dokumentation, der skal indsendes til kommunen, mindst 4 uger før et campingområde til flere end 150 personer tages i brug, og skal angive placering, indretning og brug af de enkelte delområder. Arrangementsplanen bør udarbejdes i henhold til denne vejlednings bilag 11a.~~

3.4 Opvarmning

Opvarmning af campingenheder må kun ske med elvarme~~.~~. ~~e~~Caravans kan dog opvarmes med gas eller olie, hvis der er et fastmonteret varmesystem i campingenheden.

3.5 Anvendelse af kogeapparater ~~og anvendelse af åben ild.~~

Anvendelse af kogeapparater skal så vidt muligt ske i form af apparater, der er tilsluttet elnettet. Ved anvendelse af apparater, der drives af gas, væske eller fast stof, skal kogeapparaterne indrettes og placeres, så risikoen for at en brand opstår mindskes.

Med ændringsmarkeringer i forhold til version 1.1

Kogeapparater må kun anvendes i særligt indrettede områder eller ved den enkelte campingenhedi teltområder, hvor der er krav om indbyrdes afstand på mindst 3,0 m mellem teltenecampingenhederne.

3.6 F-gas

Anvendelse af F-gas, herunder gas-grillер, må i campingområder med krav om indbyrdes afstand på mindst 3,0 m mellem campingenhederne må ske ved den enkelte campingenhed under forudsætning af, at:

- Ggasflasker, ikke har en tilladelig fyldning på mere end 11 kg.
- Dder højst anvendes 1 gasflaske pr. kogeapparat/grill.
- Dder højst er en reserveflaske pr. campingenhed.
- Ggasflasker placeres oprejst og sikres mod påkørsel og placeres oprejst.

Fastmonterede gastanke på campingenheder kan tillades, såfremt hvis de har en tilladelig fyldning på højst 40 kg. Der kan ske tilkobling fra til gasgrillер direkte fra tanken.

3.7 Kulgrillер, og bål og brug af åben ild

Bål eller gGrillер (typisk kulgrillер), bål og brug af åben ild, hvor der anvendes fast stof, skal placeres jf. *Beredskabsstyrelsens bekendtgørelse nr. 1339 af 10. december 2014 om brandværnsforanstaltninger ved afbrænding, brug af ild, lys, varmekilder m.v. (afbrændingsbekendtgørelsen)* samt Beredskabsstyrelsens vejledning hertil, der bl.a. indeholder vejledende afstande fra bål.

3.8 Håndslukningsudstyr

På campingområder skal der opsættes trykvandslukkere eller håndsprøjtebatterier samt en branddasker, så der alle steder er en ganglængde på højst 30 m fra enhver campingenhedhøjst 30 m til nærmeste campingenhed.

Ved steder, der er særligt indrettet til steder hvor der anvendeskulgrill, bål og brug af åben ild, skal der opsættes mindst en én egenet håndildslukker og et brandtæppe ved alle udgange til friområder.

Håndslukningsudstyr skal placeres, så de er synligte, let tilgængeliget og forsynet med skilte, hvilket så det nemt kan identificeres og skal sikreunderstøtte, at placeringen af håndslukningsudstyr hurtigt kan identificeres, og hurtigt kan tages i brug anvendes i tilfælde af brand.

Håndslukningsudstyr skal være i overensstemmelse med beskrivelserne i bilag 12 i denne vejledning.Håndslukningsudstyr skal opsættes og følge beskrivelserne i denne vejlednings *Bilag 12: Præ-accepterede løsninger for brandtekniske installationer og håndslukningsudstyr.*

3.9 Ordensregler for campingområder

Arrangøren eller den driftsansvarlige for arrangementet, skal sikre, for at campingområdet indrettes i overensstemmelse med bestemmelserne i dette bilag, og at nedenstående ordensregler efterleves:.

- Eventuelt personale skal være instrueret om placeringen og brugen af brandslukningsmateriellet og om, hvorledes hvordan redningsberedskabet alarmeres.
- Hvor der ikke er personale, skal der udarbejdes en brand- og evakueringsinstruks og et sæt ordensregler, der udleveres til alle brugere.
- Friområder holdes frie og ryddelige. Parkerede køretøjer, telte m.v., skal straks fjernes, så ledes at det sikres, at der ikke kan ske brandspredning mellem felterne, og så der er forsvarlige rednings- og slukningsmuligheder i tilfælde af brand.
- Der må ikke parkeres motorkøretøjer i campingområder. Autocampere og lignende campingenheder er dog undtaget.

Med anmærkninger til forhåndsversion 1.1

- Der må ikke parkeres motorkøretøjer i friområderne. Af- og pålæsning er dog tilladt.
- Brændbart affald skal anbringes i affaldscontainere af ubrændbart materiale. Affaldscontainere skal tømmes efter behov, dog mindst ~~1~~ en gang om dagen. Affaldscontainere skal placeres mindst 3,0 m fra nærmeste campingenhed.
- Møbler og lignende bræ~~a~~ndbare genstande~~,~~ må ikke medbringes i campingområder, ~~.~~ ~~U~~Uundtagent ~~herfra er~~ campingenheders faste installationer ~~samt~~ og soveposer, liggeunderlag og andet letvægtsudstyr, der normalt anvendes i forbindelse med campering.
- Brug af åben ild er kun~~ikke~~ tilladt på de ~~, bortset fra~~ steder der er særligt indrettet hertil, se afsnit *3.7.*
- Kogeapparater må kun anvendes i de ~~telt~~områder, hvor der er krav om mindst 3,0 m indbyrdes afstand mellem campingenheder~~telte~~ne, eller på dertil indrettede bålpladser.
- F-gas, herunder gas~~-~~grill må kun anvendes i områder, hvor der er krav om mindst 3,0 m indbyrdes afstand mellem campingenhederne.

Med ændringsmarkeringer i forhold til version 1.1

4 Midlertidige udendørs ~~S~~salgsområder

Dette afsnit beskriver præ-accepterede løsninger for midlertidige udendørs salgsområder på festivaler, loppemarkeder, kræmmermarkeder, julemarkeder, dyrskuer og lign. til flere end 150 personer.

Et salgsområde er et sammenhængende område i det fri, der udlægges til brug for salgsboder eller lignende, som opstilles i forbindelse med midlertidige udendørs arrangementer~~hvor der opsættes et antal salgsboder, hvorfra der sker salg~~. Salgsboder kan f.eks. bestå af:

- Almindelige borde.~~, mindre~~
- Små telte (pavilloner), salgstelte og boder opbygget i træ eller lignende ~~i forskellige størrelse~~på højst 100 m^2, hvor der primært foregår handel, og som anvendes af højst 50 personer. Personer der er tilknyttet salgsboden. skal medregnes i personantallet.~~,~~
- Foodtrucks, boder og telte, hvor der tilberedes og sælges mad fra, men hvor der ikke er ophold for kunder.~~,~~
- Campingvogne med fortelte.~~, boder opbygget i træ eller lignende.~~

En salgsbod, der anvendes af flere end 50 personer og/eller er større end 100 m^2 betragtes som et forsamlingstelt og skal overholde bestemmelserne i afsnit 2.

I salgsområder, hvor der placeres oplag~~, der er~~ omfattet af Beredskabslovgivningen, skal oplagene indrettes og placeres efter detailkravene i Beredskabslovningens bekendtgørelser. Eksempler på oplag, der kan være omfattet af Beredskabslovgivningen, er oplag der indeholder ~~bestående af~~ gasser, brandfarlige væsker eller større oplag af brandfarlige faste stoffer.

4.1 Myndighedsbehandling

4.1.1 Udendørs ~~S~~salgsområder til højst 150 personer

Salgsområder til højst 150 personer er ikke omfattet af Bygningsreglementet, jf. BR18 § 4, stk. 1, nr. 7). Personantallet bestemmes som det forventede største ~~maksimale~~ antal personer, der vil være på salgsområdet samtidigt. Personer der er tilknyttet arrangementet, salgsboder m.m. skal medregnes i personantallet.

Der er derfor ikke krav til indretning eller meddelelse til kommunalbestyrelsen af salgsområder til højst 150 personer.

4.1.2 Udendørs s~~S~~algsområder til flere end 150 personer

Salgsområder til flere end 150 personer skal overholde kravene i Bygningsreglementets ~~krav i~~ kapitel 5 - ~~b~~Brand. Personantallet bestemmes som det forventede største ~~maksimale~~ antal personer, der vil ~~være~~ opholde sig på salgsområdet samtidigt. Personer der er tilknyttet arrangementet, salgsboder m.m. skal medregnes i personantallet.

Hvis tidligere års tilladelser eller de præ-accepterede løsninger i dette bilag følges i deres~~sin~~ helhed, anses~~vil~~ kravene i *Bygningsreglementets kapitel 5 – ~~b~~Brand* for ~~udgangspunkt~~ værende overholdt.

4.1.2.1 Byggetilladelse

Salgsområder til flere end 150 personer, der følger de præ-accepterede løsninger i dette bilag som helhed, kan jf. BR18 § 6~~-~~f, stk. 2, etableres uden ansøgning om byggetilladelse, uanset personantal og areal af salgsområdet.

Hvis de præ-accepterede løsninger i dette bilag ikke følges i deres~~sin~~ helhed, skal der ansøges om byggetilladelse, og ~~skal~~ kommunalbestyrelsen skal meddele byggetilladelse, inden salgsområdet må etableres.

Med ændringsmarkeringer i forhold til VERSION 1.1

4.1.2.2 ~~*Meddelelse til kommunalbestyrelsen*~~*Teknisk sagsbehandling*

Hvis kommunalbestyrelsen i forbindelse med ansøgning om byggetilladelse vurderer, at der skal inddrages en certificeret brandrådgiver, kan ansøger i stedet vælge, at kommunalbestyrelsen foretager den tekniske sagsbehandling af brandforhold, jf. BR18 § 6f, stk. 4.

4.1.2.3 *Meddelelse til kommunalbestyrelsen*

~~Jf. § 6 f, Sstk. 3. skal~~ Meddelelse om etableringen af salgsområdet ~~der~~ til flere end 150 personer skal ~~ske~~ sendes ~~meddelelse~~ til kommunalbestyrelsen, jf. BR18 § 6f, stk. 3 ~~om etableringen af salgsområdet~~. Meddelelsen skal indeholde oplysninger om salgsområdets placering, indretning og brug, jf. *Bygningsreglementets kapitel 5 - Brand*. Meddelelsen skal være modtaget af kommunalbestyrelsen senest 4 uger før~~,~~ området tages i brug.

Oplysning om salgsområdets placering, indretning og brug sker ved at udarbejde en arrangementsplan over området. Planen skal i nødvendigt omfang suppleres med en kort beskrivelse af brugen af området.

Meddelelse til kommunalbestyrelsen skal ske, uanset om etablering~~en~~ af salgsområdet kræver byggetilladelse eller ej.

Det skal bemærkes, at de 4 uger ikke er et servicemål for kommunalbestyrelsen, og i de tilfælde, hvor der kræves en byggetilladelse, kan sagsbehandlingstiden ~~godt være længere end de~~ overstige 4 uger. Ansøger bør derfor på forhånd have orienteret sig om kommunens sagsbehandlingstid på byggesager og indsende ansøgningen i overensstemmelse hermed. Tidsfristen er ~~alene~~ kun angivet for at~~, så det~~ sikre~~s~~, at kommunalbestyrelsen og redningsberedskabet har mulighed for at planlægge eventuelle tilsyn.

~~4.1.2.3 *Teknisk sagsbehandling*~~

~~I BR18 § 6 f, stk. 4 beskrives det, at hvis det vurderes, at der skal inddrages en certificeret brandrådgiver, kan ansøger i stedet vælge, at kommunalbestyrelsen i stedet skal foretage teknisk sagsbehandling af afvigelserne fra de præ-accepterede løsninger. Den kommunale sagsbehandling skal dog kun omfatte afvigelser fra de præ-accepterede løsninger på baggrund af den dokumentation son ansøger fremsender.~~

4.1.2.4 *Certificeret statiker og brandrådgiver*

Salgsområder er undtaget fra indplacering i konstruktionsklasser jf. BR18 § 489, stk. 3. Det er dog kun indretning af områderne som helhed, der er undtaget, og ikke eventuelle telte eller andre transportable konstruktioner, der placeres i områderne. Hvis der er telte eller andre transportable konstruktioner, der ikke er certificerede og som kræver byggetilladelse, skal der enten anvendes en certificeret statiker eller foretages kommunal teknisk sagsbehandling.

Salgsområder er undtaget fra indplacering i brandklasser efter jf. BR18~~,~~ § 493, stk. 3. Det er dog kun indretning af områderne som helhed, der er undtaget, og ikke eventuelle telte eller andre transportable konstruktioner, der placeres i områderne. Det skal dog i hvert tilfælde vurderes, om der skal inddrages en certificeret brandrådgiver, og i hvor stort omfang~~,~~ der skal udarbejdes dokumentation. Denne vurdering foretages af kommunalbestyrelsen.

For salgsområder skal der ikke inddrages en certificeret brandrådgiver, hvis områderne udformes og indrettes efter de præ-accepterede løsninger i dette bilag i deres~~sin~~ helhed.

Hvis ~~der fraviges fra~~ de præ-accepterede løsninger i dette bilag fraviges, skal det på anden ~~vis~~ måde dokumenteres at *Bygningsreglementets kapitel 5 – Brand* er overholdt. ~~Denne~~ D~~d~~okumentationen ~~skal~~kan udfærdiges af en certificeret brandrådgiver~~, der skal være certificeret til mindst brandklasse 2~~. Alternativt kan ansøger vælge, at kommunalbestyrelsen skal foretage teknisk sagsbehandling af fravigelserne fra de præ-accepterede løsninger af brandforhold jf. *Bygningsreglementets kapitel 5 – Brand*. Omfanget af dokumentationen begrænser sig ~~alene~~ kun til fravigelserne~~, og der skal ikke udarbejdes start- og sluterklæring~~.

Med ændringsforslag i forhold til version 1.1

~~Af~~Fravigelser for de præ-accepterede løsninger for redningsberedskabets indsatsmuligheder kræver ikke inddragelse af en certificeret brandrådgiver, men ~~alene~~ kun~~en~~ tilladelse fra kommunalbestyrelsen.

4.2 Indretning af salgsområder

Ved i~~I~~ndretning af salgsområderne skal ~~ske, så~~ det sikres, at der ikke kan ske væsentlig brandspredning. P~~de p~~ersoner, der opholder sig i salgsområderne, herunder salgsboderne, skal på sikker vis kunne evakuere området og bringe sig selv i sikkerhed, og ~~herunder i salgsboderne, kan evakuere fra området, samt at der ikke sker væsentlig brandspredning. Det skal ligeledes sikres at~~ redningsberedskabet skal have~~har~~ mulighed for at foretage en sikker indsats.

Det skal sikres at salgsområder placeres mindst 5,0 m fra naboskel, vej- og stimidte, og at afstanden fra salgsområder til eksempelvis forsamlingstelte, campingområder, bygninger, brandfarlige oplag m.v., skal have en afstand, der mindst svarer til summen af de afstande, de hver især skal have til naboskel.

Eksempler på salgsområders afstande til bygninger og forsamlingstelte:

- En bygning med beton eller murstensfacade skal normalt holdes i en afstand på 2,5 m fra naboskel. Det betyder at afstanden mellem salgsområde og bygning skal være 5,0 m + 2,5 m = 7,5 m.
- Et forsamlingstelt skal normalt holdes i en afstand på 5,0 m til naboskel. Det betyder at afstanden mellem salgsområde og forsamlingstelt skal være 5,0 m + 5,0 m = 10,0 m.
- En bygning med et stråtag skal normalt holdes 10,0 m fra naboskel. Det betyder at afstanden mellem salgsområde og bygning med stråtag skal være 10,0 m + 5,0 m = 15,0 m.

4.2.1 Opdeling af salgsområder

For at sikre mod væsentlig brandspredning på salgsområder, skal salgsområdet opdeles i felter på ~~med en størrelse af~~ højst 1.000 m^2, og felterne skal placeres med en afstand, der sikrer, at en brand ikke kan brede sig fra et felt til et andet.

Felternes størrelse beregnes som det areal, der afgrænses af de enkelte salgsboder~~,~~ inklusiv eventuelle bagområder og udstillinger foran salgsboden.

Ved bestemmelse af felternes størrelse regnes friområderne mellem salgsområder ikke med til felternes areal.

I salgsområder skal der mellem hvert felt på 1.000 m^2 være friområder, som er mindst 10,0 m brede. Friområderne kan anvendes til evakuering ud af salgsområdet.

Inden for felter på 1.000 m^2 kan salgsboder opstilles i ubrudt række. Der er derfor ikke krav til længden på en ubrudt facadelængde.

Afstanden mellem salgsområderne kan reduceres til 5,0 m, hvis:

- Salgsbodernes facader udføres af materialer mindst som klasse B-s2,d0 [Klasse A materiale] (Gipsplader, brandimprægneret træ, og lignende).
- Salgsboderne udføres som åbne salgsboder og åbne fortelte til campingvogne. Det forudsættes, at salgsboder og fortelte er åbne i mindst halvdelen af facadearealet.
- Salgsbodernes facader afbrydes pr. mindst 25,0 m, og når afstanden mellem salgsbodernes brudte facader samtidig er mindst 10,0 m.

~~For at der ikke sker brandspredning mellem felterne skal det sikres at facaderne er udført en af følgende muligheder:~~

Med ændringsmarkeringer for høring til version 1.1

- ~~I materialer som svarer til mindst B-s1,d0 [Klasse A materiale] (Gipsplader, brandimprægneret træ, og lign.)~~
- ~~Som åbne salgsboder, fortelte til campingvogne, pavilloner, eller telte på op til 50 m².~~ ~~Det forudsættes dog at telte og pavilloner er åbne i mindst halvdelen af facadelængden.~~

~~Afstanden mellem felterne skal dog være mindst 10,0 m hvis der etableres ubrudte facader med en længde på mere end 25 m bestående af:~~

- ~~Lukkede telte på mere end 50 m².~~
- ~~Facader udført i materialer ringere end klasse B-s1,d0 [Klasse A materiale].~~
- ~~Lukkede campingvogne, letvogne eller lignende.~~

~~Det skal sikres at salgsområder placeres mindst 5 m fra skel, og at afstanden fra salgsområder til eksempelvis forsamlingstelte, campingområder, bygninger, brandfarlige oplag m.v., skal have en afstand der mindst svarer til summen af de afstande de hver især skal have til naboskel.~~

~~Eksempler på indbyrdes afstande:~~

- ~~En bygning med beton eller murstensfacade skal normalt holdes i en afstand på 2,5 m fra naboskel. Det betyder at afstanden mellem salgsområde og bygning skal være 5,0 m + 2,5 m = 7,5 m.~~
- ~~Et forsamlingstelt skal normalt holde en afstand på 5,0 m til naboskel. Det betyder at afstanden mellem salgsområde og bygning skal være 5,0 m + 5,0 m = 10,0 m.~~
- ~~En bygning med et stråtag skal normalt holdes 10,0 m fra naboskel. Det betyder at afstanden mellem salgsområde og bygning skal være 10,0 m + 5,0 m = 15,0 m.~~

~~I salgsområder skal der mellem hvert felt på 1.000 m² være friområder, som er mindst 5 m brede. Friområderne kan anvendes som flugtvejsarealer ud af det område, der er er udlagt f.eks. som markedsplads.~~

~~Denne bredde vurderes at være tilstrækkelig for, at personer kan flygte væk fra det område, der kan være opstået brand i og videre til et område, hvor de ikke bliver påvirket af røg eller varme.~~

~~Ved bestemmelsen af felternes størrelse regnes friområderne ikke med til felternes areal.~~

4.3 Udarbejdelse af planer for salgsområder

~~Hvis d~~Der skal udarbejdes en målfast plan for salgsområdet som dokumentation for placering, indretning og brug jf. BR18 § 6-f, stk. 3.~~ bør p~~Planen bør mindst vise:~~ følgende:~~

- Størrelse og placering af felter med salgsområder.
- Friområder mellem felter med salgsområder, herunder friområder der anvendes til evakueringflugtveje. Det skal fremgå, hvor brede friområderne er.
- Oplag af gasser og brandfarlige væsker.
- Brandslukningsmateriel.
- Placering og brug af kogeapparater, herunder grill og friture, bortset fra el~~kogeplader~~, i og ved salgsboder.
- Affaldsbeholdere med et rumindhold på mere end 1 m³.
- Redningsberedskabets indsatsmuligheder.

~~Ved arrangementer der omfatter forsamlingstelte, camping- og salgsområder, og eventuelt andre områder, der ikke er omfattet af dette bilag, såsom koncertområder foran scener, forlystelser, parkeringsarealer m.m. skal der udarbejdes en arrangementsplan, der giver et samlet overblik over de enkelte områder, og redningsberedskabets muligheder for at kunne komme frem på området.~~

Med ændringsmarkeringer i forhold til version 1.1

~~Arrangementsplanen er en del af den dokumentation, der skal indsendes til kommunen, mindst 4 uger før et forsamlingstelt, camping- eller salgsområde til flere end 150 personer tages i brug, og skal angive placering, indretning og brug af de enkelte delområder. Arrangementsplanen bør udarbejdes i henhold til denne vejlednings bilag 11a.~~

4.4 Udgange og flugtveje

4.4.1 Fra salgsboder

For at sikre, at de personer, der opholder sig i salgsboder, kan komme hurtigt ud af salgsboderne, skal de have mindst én udgang direkte til det fri med en bredde på mindst 0,77 m.~~Hvis personbelastningen i en salgsbod er højst 50 personer, og salgsboden har et areal, der er højst 150 m², skal der være mindst én flugtvej fra salgsboden ud til friområderne.~~

~~Hvis personbelastningen i salgsboden er mellem 50 og 150 personer, og salgsboden har et areal, der er mindre end 150 m², skal der være mindst to flugtveje fra salgsboden ud til friområder, og de to flugtveje skal være placeret i bodens modstående ender.~~

~~Hvis personbelastningen er større end 150 personer eller salgsboden er større end 150 m², skal retningslinjerne for flugtveje fra telte anvendes(henvisning).~~

4.4.2 Fra salgsområder

Friområderne mellem flere salgsområder kan anvendes til evakuering, så det er muligt at komme ud af det område, der er udlagt som flere samlet salgsområder.

~~I salgsområder skal der mellem hvert felt på 1.000 m² være friområder, som er mindst 5 m brede. Friområderne kan anvendes som flugtvejsareal, så det er muligt at evakuere ud af det område, der er udlagt som salgsområde.~~

~~Bredden på 5,0 vurderes at være tilstrækkelig til, at personer kan evakuere fra det område, hvor der kan være opstået brand, og videre til et område, hvor personer ikke bliver påvirket af røg eller varme.~~

Såfremt et salgsområde benyttes i tidsrummet mellem solnedgang og solopgang, og området er omgivet af hegn eller lignende, skal hver udgang fra området være forsynet med ~~belyste~~ flugtvejsbelysning~~skilte~~.

Placering og udførelse af flugtvejsbelysning skal ske ved at følge retningslinjerne i denne vejlednings *Bilag 12: Præ-accepterede løsninger for brandtekniske installationer og håndslukningsudstyr.*

~~4.4.3 fra bilag 12 i denne vejledning.~~

~~4.4.4~~4.4.3 Opvarmning

Opvarmning af salgsboder må kun ske med elvarme og F-gasanlæg.

Der må højst anvendes 1 gasflaske pr. opvarmningssted, se i øvrigt afsnit 4.6.

4.5 Anvendelse af kogeapparater~~ og anvendelse af åben ild~~

Anvendelse af kogeapparater skal så vidt muligt ske i form af apparater, der er tilsluttet elnettet. Ved anvendelse af apparater, der drives af gas, væske eller fast stof, skal kogeapparaterne være godkendt til dette~~,~~ og placeres, så risikoen mindskes for at en brand opstår ~~mindskes~~.

4.6 F-gas

Anvendelse af F-gas, herunder til gas~~-~~grill~~er~~ og opvarmning~~,~~ i salgsboder, må ske i felter på 1.000 m², hvor der også er andre salgsboder under forudsætning af, at~~:~~

- D~~d~~er højst anvendes 1 gasflaske pr. kogeapparat/grill.

Med anmærkninger i forhold til version 1.1

- Ggasflasker, der er placeret inde i salgsboderne, ikke har en tilladelig fyldning på mere end 11 kg.
- Eeventuelle reservegasflasker opstilles i det fri.
- Ggasflasker placeres oprejst og sikres mod påkørsel ~~og placeres oprejst~~.
- Ggasflasker med en tilladelig fyldning på over 11 kg ~~skal~~ anbringes i det fri, afskærmet fra publikum.
- ~~Dat d~~et samlede gasoplag pr. felt på 1.000 m^2 højst er ~~på~~ 100 gasoplagsenheder (GOE) inkl. beholdere i brug.
- ~~Hvis ovenstående ikke opfyldes, henvises der til Beredskabsstyrelsens tekniske forskrifter for gasser.~~

4.7 Kulgrill, bål og brug af åben ild

~~Bål eller g~~Grill~~er~~ (typisk kulgrill~~er~~), bål og brug af åben ild, hvor der anvendes fast stof, skal placeres jf. *Beredskabsstyrelsens bekendtgørelse nr. 1339 af 10. december 2014 om brandværnsforanstaltninger ved afbrænding, brug af ild, lys, varmekilder m.v. (afbrændingsbekendtgørelsen)* samt Beredskabsstyrelsens vejledning hertil, der bl.a. indeholder vejledende afstande fra bål.

4.8 Håndslukningsudstyr

På salgsområder skal der opsættes trykvandslukkere eller håndsprøjtebatterier ~~samt branddaskere, såfremt arealet er udlagt på græs~~, så der alle steder er en ganglængde på højst 30 m fra enhver salgsbod~~højst 30 m til nærmeste enhed~~.

I salgsboder med rumopvarmning, kogeapparater og lign. skal der opsættes mindst en egnet håndildslukker ~~og et brandtæppe ved alle udgange til friområder~~.

Håndildslukkere skal placeres synligt, let tilgængeligt og forsynes med skilte, så de nemt ~~er synlige, let tilgængelige og forsynet med skilte, hvilket skal sikre, at placeringen af håndildslukkere hurtigt kan identificeres, og at håndildslukkere hurtigt~~ kan identificeres og ~~anvendes~~ tages i brug i tilfælde af brand.

Håndildslukkere skal følge ~~være i overensstemmelse med~~ beskrivelserne i denne vejlednings Bilag 12: Præ-accepterede løsninger for brandtekniske installationer og håndslukningsudstyr.

~~4.8.1 i bilag 12 i denne vejledning.~~

~~4.8.2~~4.8.1 Ordensregler for salgsområder

Følgende ordensregler skal efterleves, og alle der har tilknytning til salgsområdet, skal orienteres om ordensreglerne:

- Friområder holdes frie for udstillede varer, oplag m.v.
- Salgsboders bagområder skal afspærres forsvarligt for publikum~~.~~
- Brug af åben ild er kun tilladt ~~forbudt undtagen~~ på særligt indrettede områder, se afsnit 4.7.
- Brændbart affald skal anbringes i affaldscontainere af svært antændeligt materiale. Affaldscontainere skal tømmes efter behov, dog mindst 1 gang om dagen~~.~~
- Der kan altid i eller ved den enkelte salgsbod placeres én affaldscontainer med et rumindhold på højst 1 m^3 til brug for mindre mængder af affald, herunder brændbart affald.
- Motorkøretøjer må ikke parkeres i salgsområder, ~~. U~~undtagen~~t herfra er~~ et motorkøretøj~~,~~ med direkte tilknytning til salgsboden. ~~Motorkøretøjer, der fungerer som salgsboder, skal medregnes i antallet.~~
- ~~Det er tilladt at maksimalt~~ Højst 2 personer med tilknytning til den enkelte salgsbod kan overnatte i salgsboden.

Med ændringsmarkeringer i forhold til version 1.1

- Der skal i hver salgsbod, hvori ~~der~~ personer overnatters, opsættes en røgalarm. Hvis ~~der~~ overnatning sker ~~tes~~ i en campingenhed (campingvogn, autocamper, telt eller lign.), skal røgalarmen placeres her.
- Der skal være ~~en~~ et runderende ~~vagt~~ tilsyn i salgsområder, hvor der overnattes. Der skal ske kontinuerlig rundering i tidsrummet 22.00 – 08.00.

Hvis der sker overnatning i felter, hvor der kan være særlig risiko for antændelse, ~~herunder kogeapparater og griller,~~ skal følgende sikres:

- Åben ild være slukket~~.~~
- Alle kogeapparater skal være slukkede og forsvarligt afbrudt~~.~~
- Ingen brandfarlige oplag omfattet af Beredskabsstyrelsens tekniske forskrifter, bortset fra op til 100 kg F-gas~~, At der i felter hvor der overnattes ikke er brandfarlige oplag, der er omfattet af Beredskabsstyrelsens tekniske forskrifter, bortset fra op til 100 kg F-gas.~~.
- Alle gasinstallationer skal være frakoblet kogeapparatet.
- Gasflasker skal være afmonteret fra apparater og ventiler skal være lukket.
- Alle tomme gasflasker skal fjernes ~~fra felterne~~.
- Alle kulgrill~~er~~ skal være helt slukket ~~inden der sker overnatning~~.

Det er den~~t~~ runderende ~~vagt~~tilsyn, der skal påse ovenstående forhold, og derfor skal denne være instrueret i hvilke steder, der er særlig risiko for antændelse.

Med ændringsmarkeringer i forhold til version 1.1

5 Drift, kontrol og vedligehold

Af BR18 § 156 fremgår det at drift, kontrol og vedligehold af midlertidige camping- og salgsområder til flere end 150 personer samt af transportable konstruktioner til flere end 150 personer, skal ske på en sådan måde, at BR18 §§ 137-142 og § 157 til enhver tid er overholdt.

Derudover skal der jf. BR18 §157 udarbejdes følgende:

- En driftsjournal og en pladsfordelingsplan til forsamlingstelte til flere end 150 personer.
- En brand- og evakueringsinstruks.
- Ordensregler om forebyggelse af brand.

Midlertidige udendørs cCamping- og salgsområder samt transportable konstruktioner skal således i hele opstillingsperioden dets levetid overholde det overordnede personsikkerhedsniveau, som beskrevet i *Bygningsreglementets kapitel 5 – Brand*skal opnås i brandsikkerhedsmæssig henseende.

I BR18 §141 fremgår det at bBrandtekniske installationer og håndslukningsudstyr skal løbende skal kontrolleres og funktionsafprøves, jf. BR18 § 141. Dette kan sikres ved at følge retningslinjerne i denne vejlednings *Kkapitel 7: Drift-, kontrol- og vedligehold af brandforhold i og ved bygninger* i denne vejledning.

~~Derudover skal der jf. BR18 §157 udarbejdes følgende:~~

- ~~En driftsjournal og en pladsfordelingsplan til forsamlingstelte til flere end 150 personer.~~
- ~~En brand- og evakueringsinstruks.~~
- ~~Ordensregler om forebyggelse af brand.~~

Den driftsansvarlige (ofte arrangøren) for arrangementet skal sikre at ovenstående er udarbejdet og at eventuelt personale er instrueret i de udarbejdede ordensregler, brand- og evakueringsinstruks, placering og brug af håndslukningsudstyr og brandtekniske installationer.

5.1 Driftsjournal

For forsamlingstelte til flere end 150 personer skal sikrer den driftsansvarlige (ofte arrangøren) sikre, at der føres en driftsjournal over kontrollen af de forhold, der fremgår af nedenstående punkter. Af driftsjournalen skal det fremgå, at kontrollen af de enkelte punkter er udført. Arrangøren eller dDen driftsansvarlige kontrollerer ved angivelse af navn, adresse, dato og klokkeslæt i driftsjournalen, at kontrollen er foretaget umiddelbart inden arrangementets start. Såfremt arrangementet varer i mere end 24 timer, gentages kontrollen for hver påbegyndt 24. time.

Før enhver benyttelse kontrolleres, at det:

- FAt flugtspassager er frie og ryddelige i hele deres bredde.
- UAt udgange kan passeres i flugtretningen uden brug af nøgle eller særligt værktøj.
- FAt flugtvejsdøre samt flugtvejsbelysning og/eller skilte ved flugtvejsdørene er synlige og følger retningslinjerne i denne vejlednings *Bilag 12: Præ-accepterede løsninger for brandtekniske installationer og håndslukningsudstyr*.tændte.
- IAt flugtvejsbelysning lyser klart og tydelig.
- At internt varslingsanlæg eller lydanlæg, der benyttes til varsling, er funktionsdueligt.
- OAt opslag med angivelse af det største maksimale antal personer er anbragt på et synligt sted.
- IAt inventaropstilling er i overensstemmelse med den til formålet, godkendte pladsfordelingsplan.

Med anmærkninger i forhold til version 1.1

- HAt håndildslukningsudstyr ~~(håndildslukker, branddasker og brandtæpper)~~ er korrekt placeret.
- BAt brandslukningsmateriel er efterset.
- Ordensregler er overholdt.

Enhver mangel, der konstateres ved udførelse af ovenstående kontrol, afhjælpes omgående.

I denne vejlednings *Kapitel 7: Drift-, kontrol- og vedligehold af brandforhold i og ved bygninger* er givet eksempler på driftsjournal samt brand- og evakueringsinstruks.

5.2 Brand- og evakueringsinstruks

Arrangøren eller den driftsansvarlige udarbejder til brug for personalet en brand- og evakueringsinstruks, der som minimum indeholder oplysning om, hvordan:~~:~~

- Ppersoner varsles.
- R~~r~~edningsberedskabet alarmeres.
- P~~p~~personalet adviseres om den opståede nødsituation.
- P~~p~~personalet vejleder gæsterne til udgangene.
- S~~s~~lukningsmateriellet bemandes og anvendes.
- H~~h~~vor og hvordan redningsberedskabet informeres

Derudover skal brand- og evakueringsinstruksen til forsamlingstelte til fl~~m~~ere end 150 personer eventuelt suppleres med, hvordan:

- O~~o~~rienteringslys tændes.
- O~~o~~ptræden og musik stoppes.
- R~~r~~øgmaskiner og andet udstyr, som medfører reduceret sigtbarhed, afbrydes.
- L~~l~~ydanlæg anvendes til orientering af gæsterne om situationen.

Brand- og evakueringsinstruksen ophænges steder, hvor personalet færdes.

Arrangøren skal sikre, at der er retningslinjer for ~~personale til~~ at tage imod redningsberedskabet. Hvor der er personale tilstede, skal personalet skal være instrueret i denne opgave. ~~Personale skal være instrueret i denne opgave, der ligeledes fremgår af Brand- og evakueringsinstruksen.~~ Personalet skal assistere beredskabet med informationer om evakueringen, igangsatte tiltag fra personalets side, guide beredskabet hen til området mv.

5.3 Ordensregler om forebyggelse af brand

Der skal udarbejdes et opslag med ordensregler om forebyggelse af brand, så~~dan at~~ brugerne, den driftsansvarlige og~~et~~ evt. personale kan minimere risikoen for antændelse af en brand.

Opslaget kan indeholde nedenstående, og skal tilpasses de aktuelle forhold. Der kan også være andre relevante punkter, der ~~er relevante, men som~~ ikke er på nedenstående liste:

- Vær forsigtig med anvendelse af åben ild.
- Levende lys og dekorationer skal anbringes på ubrændbart og stabilt underlag og i god afstand fra gardiner og andet brændbart materiale. Tændte lys skal holdes under opsyn.
- Tobaksrygning må kun finde sted på ~~inden for~~ de dertil anviste områder.
- Tobaksaffald skal opsamles i ubrændbare beholdere med låg. Beholderne må kun benyttes til dette formål.
- Affaldssække og lignende skal dagligt fjernes og anbringes i et særligt affaldsrum eller i en container.
- Duge, servietter og lignende skal ved aftagning efterses for gløder fra tobaksrygning m.v. og skal anbringes, så en eventuel brand i materialet ikke kan brede sig.

Med ændringsmarkeringer i forhold til version 1.1

- Kaffemaskiner, strygejern og lignende elektriske apparater skal ~~altid~~ afbrydes ved stikkontakten efter brug~~en~~.
- Olieklude m.v. kan selvantænde og skal efter brug~~en~~ anbringes i ubrændbar beholder med låg.
- Brandfarlige væsker (f.eks. benzin, petroleum, acetone og sprit) skal anvendes med forsigtighed og opbevares i tillukkede beholdere.
- Selvlukkende døre må kun stå åbne, hvis de ved brand lukker automatisk.
- Flugtvejsdøre må ikke spærres, og der må ikke anbringes genstande eller effekter i flugtveje og på trapper.
- Linnedvogne, rengøringsvogne og lignende må ikke ~~henstilles~~ anbringes i flugtveje.
- Brandslukningsmateriellet skal holdes frit tilgængeligt.

6 Redningsberedskabets indsatsmuligheder

6.1 Midlertidige arrangementer

Indretning af udendørsarrangementer skal ske under hensyntagen til, at der i tilfælde af brand er forsvarlig mulighed for, at redningsberedskabet kan foretage redning og ~~kan~~ bistå evakuering af personer. Det skal sikres, at det nødvendige slukningsarbejde~~r~~ kan gennemføres ~~det slukningsarbejde, der er nødvendig hertil samt~~ og at der er den nødvendige afstand mellem brandmæssige enheder til at begrænse væsentlig brandspredning mellem områderne.

Det kommunale redningsberedskab kan endvidere i medfør af Beredskabslovens § 35, stk. 3, stille supplerende ~~vilkår~~ krav ~~til~~ f.eks. til områder, hvor mange mennesker forsamles i det fri~~,~~ eller til den overordnede infrastruktur.

Ved udendørsarrangementer skal der derfor udlægges brandveje, så redningsberedskabet kan køre frem med deres køretøjer og foretage en forsvarlig slukningsindsats. Brandvejene skal udlægges, så der fra brandvejen til ethvert sted på området er en gang~~linj~~længde på højst 80 m, og så redningsberedskabet kan benytte traditionelle slangeudlægninger.

Brandvejene skal have en bredde på minimum 3,0 m og skal være friholdt i en højde på mindst 3,4 m. Brandvejene må godt være sammenfaldende med de udlagte friområder. Brandvejene skal være befæstede~~t~~ og kørefaste, så redningsberedskabernes køretøjer kan komme frem.

I forbindelse med slukningskøretøjernes tilkørsel skal der være mulighed for, at indsatspersonel kan stige ud af køretøjerne, samt udtage udstyr (slanger, værktøj og lign.) fra slukningskøretøjernes sideskabe. I de områder hvor redningsmandskabet skal stige ud af slukningskøretøjerne, skal brandvejen have en bredde på mindst 5,0 m svarende til den mindste afstand mellem de forskellige områder.

Der er ikke krav om, at brandvejene er skiltet, men det skal klart fremgå, hvilke veje der er brandveje.

~~Nedenstående er et eksempel på en arrangementsplan, som på efterfølgende side er i størrelsesforhold 1:2.000, og som kan være på en A3.~~ Arrangementsplanen bør udarbejdes i henhold denne vejlednings *Bilag 11a: Vejledning om arrangementsplaner for midlertidige udendørsarrangementer*, hvor der er angivet et eksempel på en arrangementsplan.


6.2 Øvrig bebyggelse~~Eksisterede byggeri~~

Når der opsættes forsamlingstelte~~,~~ ~~og~~ ~~andre~~ transportable konstruktioner, eller der ~~og~~ etableres camping- eller ~~og~~ salgsområder, må redningsberedskabets indsatsmuligheder i forbindelse med øvrig ~~eksisterende~~ bebyggelse~~byggeri~~ ikke forringes eller forhindres. Det betyder blandt andet, at der~~man~~ ikke må opsættes konstruktioner, der spærrer brandveje, ligesom ~~man~~der ikke må opsættes konstruktioner på steder, der er udlagt til eller forudsat

Med anmærkninger i forhold til version 1.1

som eksempelvis brandredningsarealer for opsætning af redningsberedskabets stiger. Brandhaner og andre installationer, der kan benyttes af redningsberedskabet, må ~~heller~~ ikke afspærres eller gøres utilgængelige.

~~6.3 Arrangementsplan~~

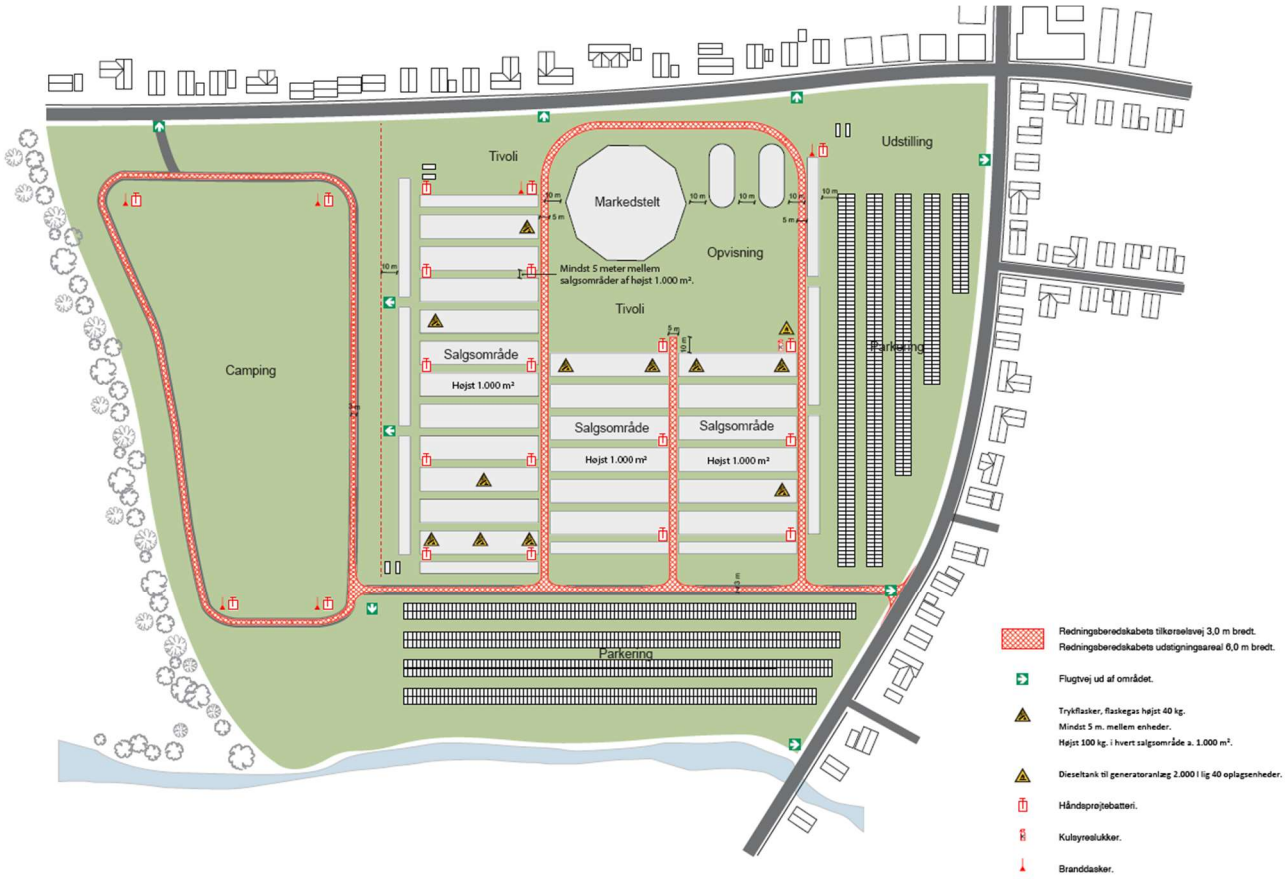

Med ændringsmar

Anneks A Tabel til forsamlingstelte til private formål

Areal	Højst 150 m²	Højst 150 m²	Over 150 m²	Over 150 m²
Personer[1)]	51 – 150	151 – 1.000	51 – 150	151 – 1.000
Anvendelseskategori	3			
Risikoklasse	1	2	2	2
Brandklasse	BK1	BK2	BK2	BK2
Varighed højst	6 uger			
Krav om byggetilladelse.	Nej[3)]			
Krav om indplacering i brandklasse/certificeret brandrådgiver	Nej[3)]			
Meddelelse med oplysning om indretning og brug sendes til kommunalbestyrelsen	Nej	4 uger før brug	Nej	4 uger før brug
Brandbelastning	Højst 800 MJ/m²			
Antal udgange 151-350 pers.[2)] 351-550 pers. [2)] 551-750 pers. [2)] 751-950 pers. [2)] 951-1.000 pers[2)]	2	3 4 5 6 7	2	3 4 5 6 7
Pladsfordelingsplan	Nej	Ja	Nej	Ja
Placering fra skel	Mindst 5,0 m			
Afstand til salgs-/campingområde og bygning	Afstand, der mindst svarer til summen af de afstande, de hver især skal have til naboskel			
Afstand til sekundær bebyggelse	Mindst 5,0 m			
Krav til teltdug	Nej	Ja	Nej	Ja
Krav til bær. konstruktioner	Nej			
Krav om varsling	Nej	Nej ikke såfremt der er lydanlæg eller megafon	Nej	Nej ikke såfremt der er lydanlæg eller megafon
Krav om flugtvejs- og panikbelysning	Nej	Nej ikke såfremt teltet ikke anvendes efter mørkets frembrud	Nej	Nej ikke såfremt teltet ikke anvendes efter mørkets frembrud
Brandslukningsudstyr	Nej	Trykvandslukkere eller håndsprøjtebatterier pr. min. 30 m	Nej	Trykvandslukkere eller håndsprøjtebatterier pr. min. 30 m
Ordensregler	Nej	Ja	Nej	Ja

[1)] Forsamlingstelte, der placeres med en indbyrdes afstand mindre end 5,0 m, betragtes som ét telt i forbindelse med fastlæggelse af personantallet.

[2)] Mindst 10 mm pr. person.

[3)] Når dette bilag følges i sin helhed.

Med ændringsmarkeringer i forhold til version

Anneks B Tabel til forsamlingstelte til ikke private formål

Areal	Højst 100 m²	100 – 150 m²	100 – 150 m²	Over 150 m²	Over 150 m²
Personer[1)]	51 – 150	51 – 150	151 - 1000	51 – 150	151 - 1000
Anvendelseskategori	3				
Risikoklasse	1	1	2	2	2
Brandklasse	BK1	BK1	BK2	BK2	BK2
Varighed højst	6 uger				
Krav om byggetilladelse.	Nej[2)]	Ja – dog ikke[3)]	Ja – dog ikke[3)]	Ja – dog ikke[3)]	Ja – dog ikke[3)]
Krav om indplacering i brandklasse/certificeret brandrådgiver	Nej[2)]	Ja – dog ikke[3)]	Ja – dog ikke[3)]	Ja – dog ikke[3)]	Ja – dog ikke[3)]
Meddelelse med oplysning om indretning og brug sendes til kommunalbestyrelsen	Nej	Nej	4 uger før brug	Nej	4 uger før brug
Brandbelastning	Højst 800 MJ/m²				
Antal udgange 151-350 pers.[4)] 351-550 pers. [4)] 551-750 pers. [4)] 751-950 pers. [4)] 951-1000 pers.[4)]	2	2	3 4 5 6 7	2	3 4 5 6 7
Pladsfordelingsplan	Nej	Nej	Ja	Nej	Ja
Placering fra skel	Mindst 5 ,0 m				
Afstand til salgs-/campingområde og bygning	Afstand, der mindst svarer til summen af de afstande, de hver især skal have til naboskel				
Afstand til sekundær bebyggelse	Mindst 5,0 m				
Krav til teltdug	Nej	Nej	Ja	Nej	Ja
Krav til bær. konstruktioner	Nej				
Krav om varsling	Nej	Nej	Nej ikke såfremt der er lydanlæg eller megafon	Nej	Nej ikke såfremt der er lydanlæg eller megafon
Krav om flugtvejs- og panikbelysning	Nej	Nej	Nej ikke såfremt teltet ikke anvendes efter mørkets frembrud	Nej	Nej ikke såfremt teltet ikke anvendes efter mørkets frembrud
Brandslukningsudstyr	Nej	Nej	Trykvandslukkere eller håndsprøjtebatterier pr. min. 30 m	Nej	Trykvandslukkere eller håndsprøjtebatterier pr. min. 30 m
Ordensregler	Nej	Nej	Ja	Nej	Ja

1) Forsamlingstelte, der placeres med en indbyrdes afstand mindre end 5,0 m, betragtes som ét telt i forbindelse med fastlæggelse af personantallet.

2) Når dette bilag følges i sin helhed.

3) Hvis telte er certificeret i henhold til bekendtgørelse om certificeringsordning for transportable konstruktioner og ikke anvendes til overnatning.

4) Mindst 10 mm pr. pers.

Med ændringsmarkeringer i forhold til version